







ELEVATION-STEEL TRUSS R-F1

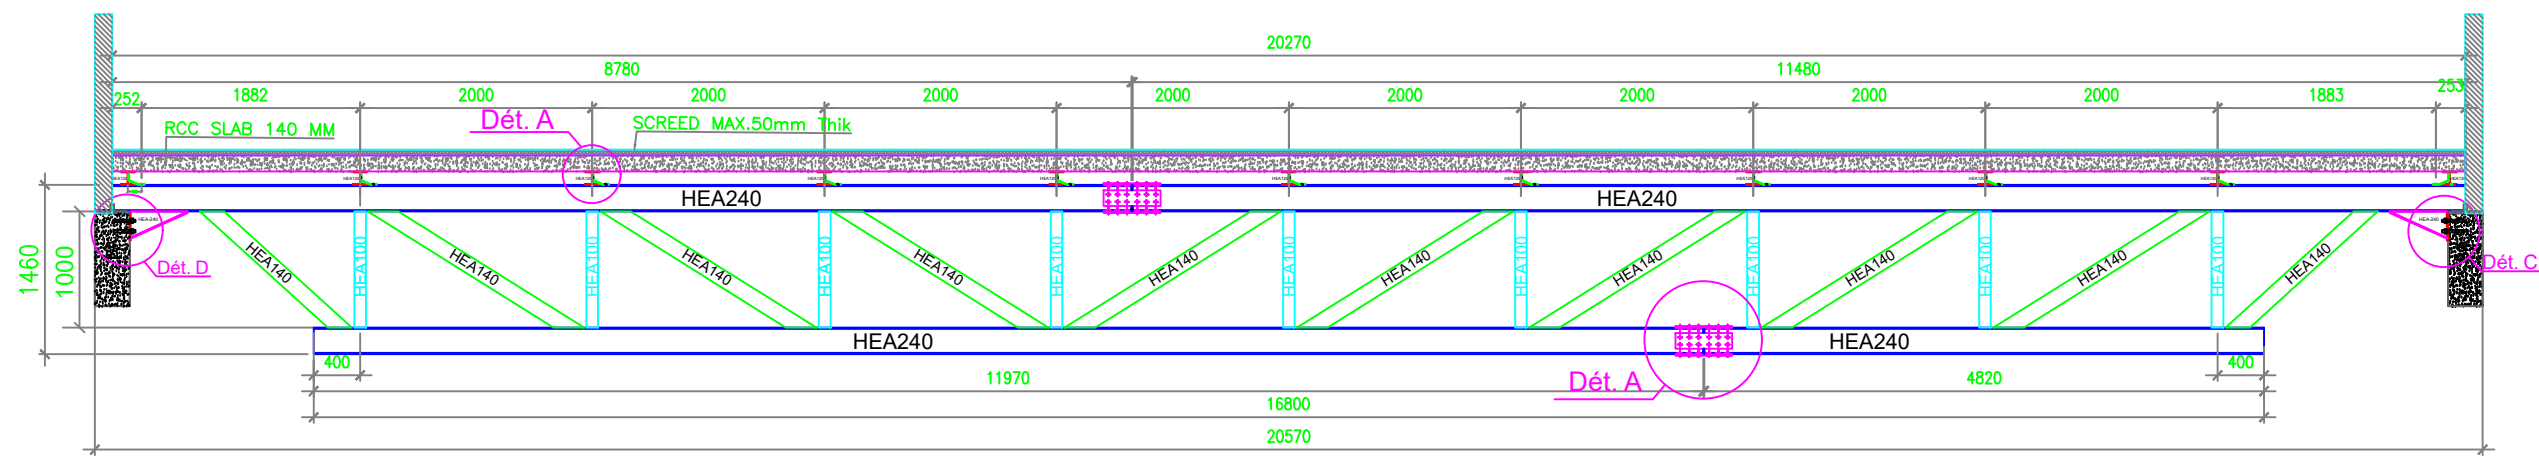

UPPER ROOF AUDITORIUM FRAMING

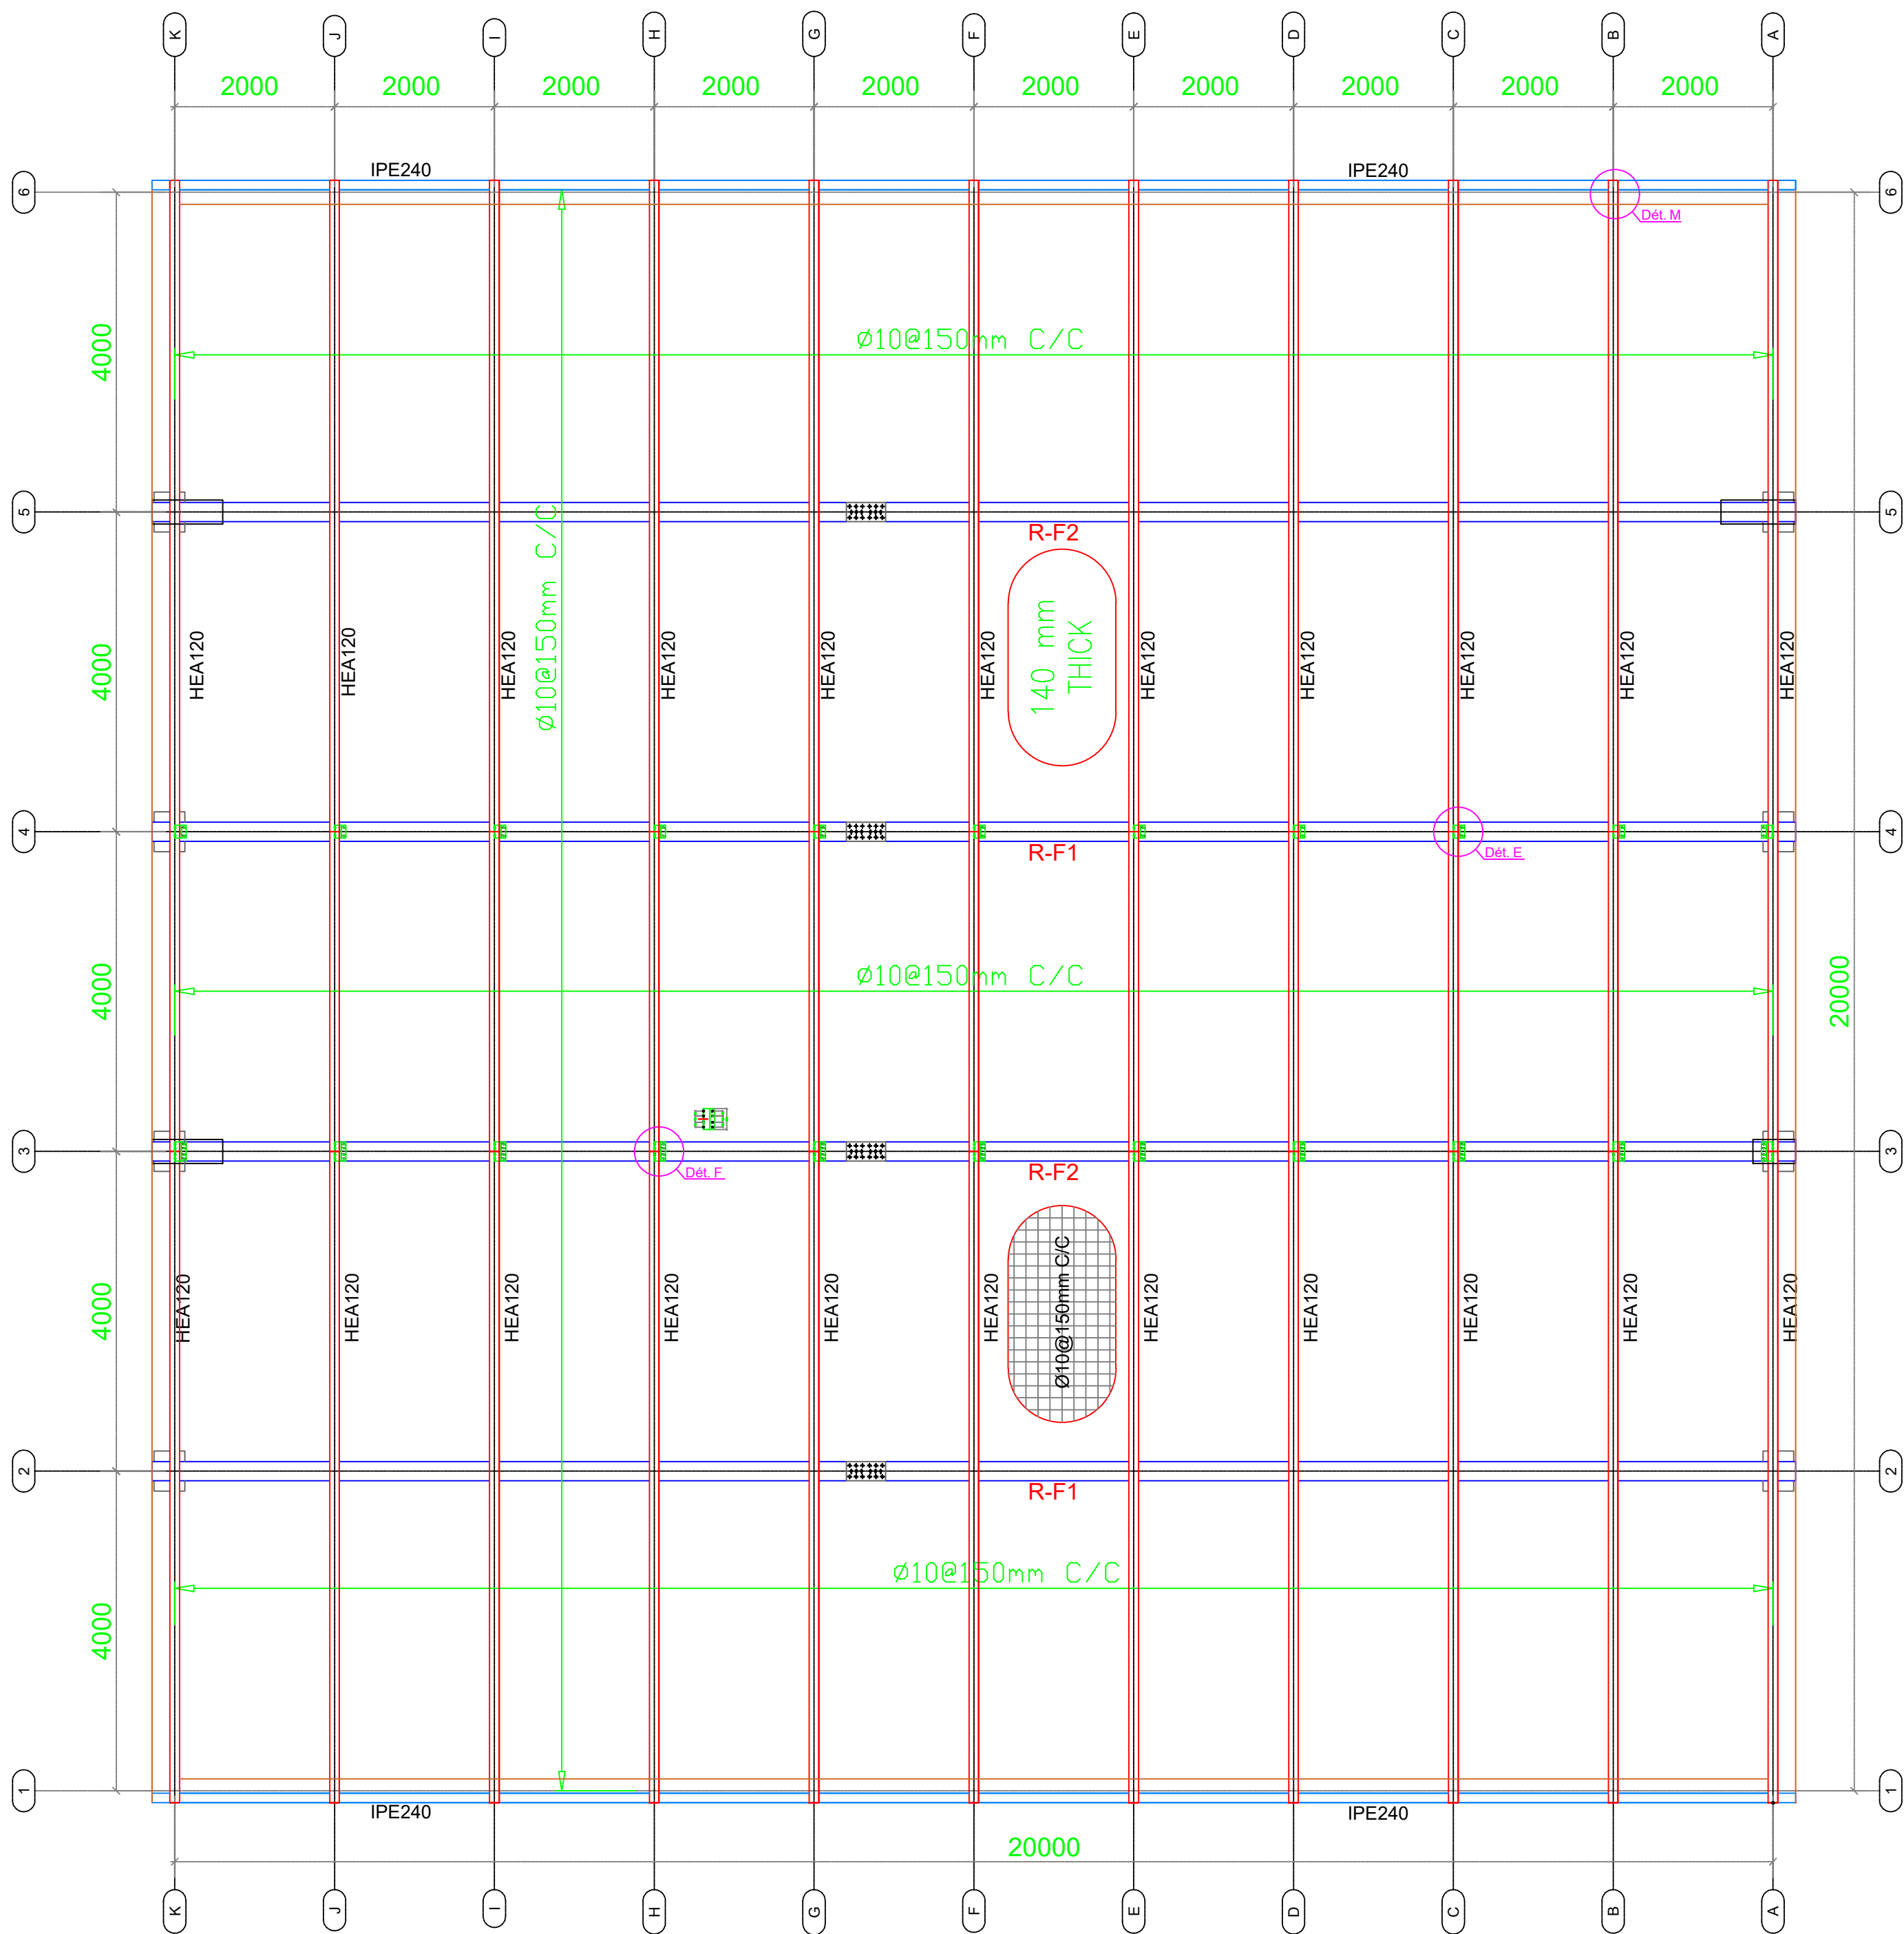

ELEVATION-STEEL TRUSS R-F2

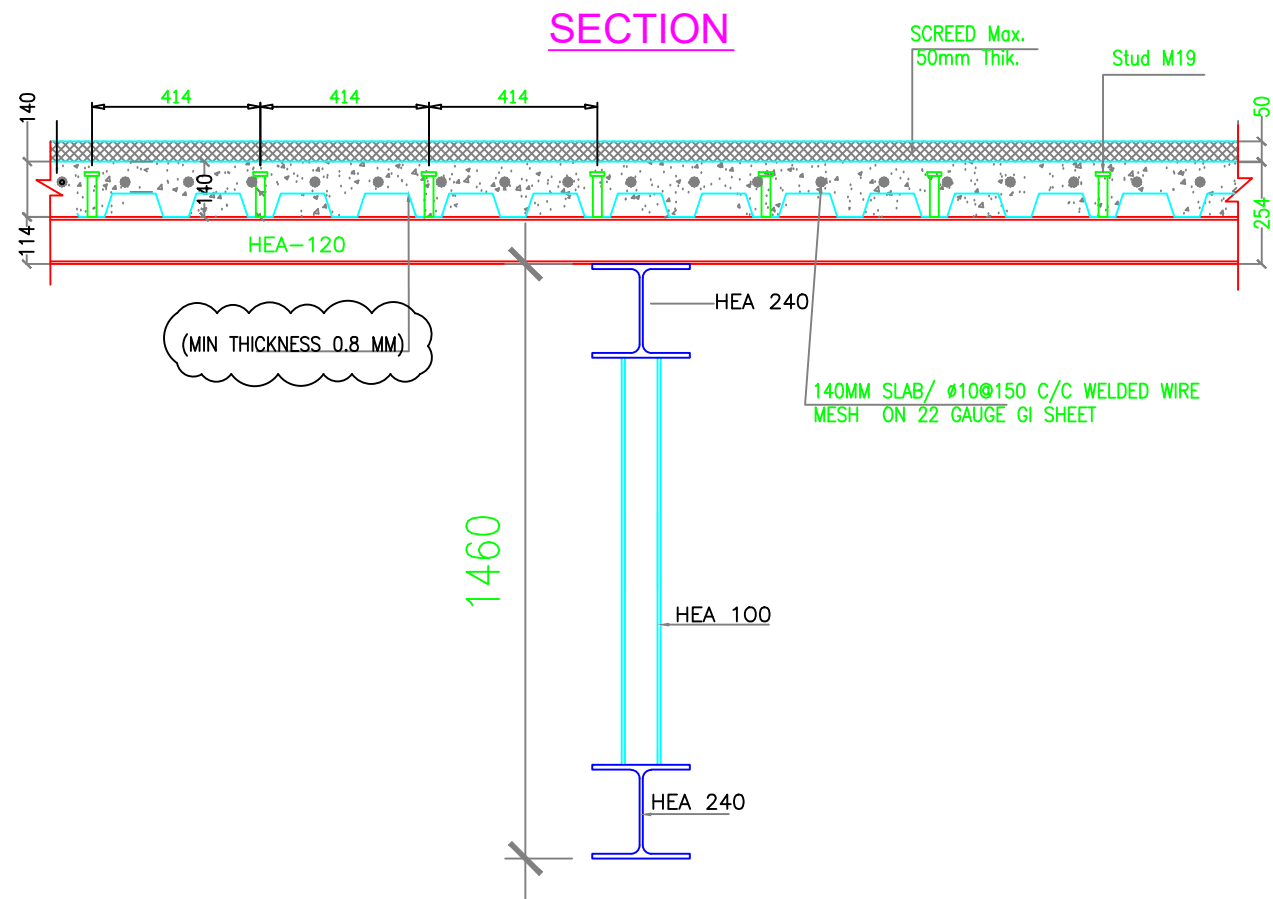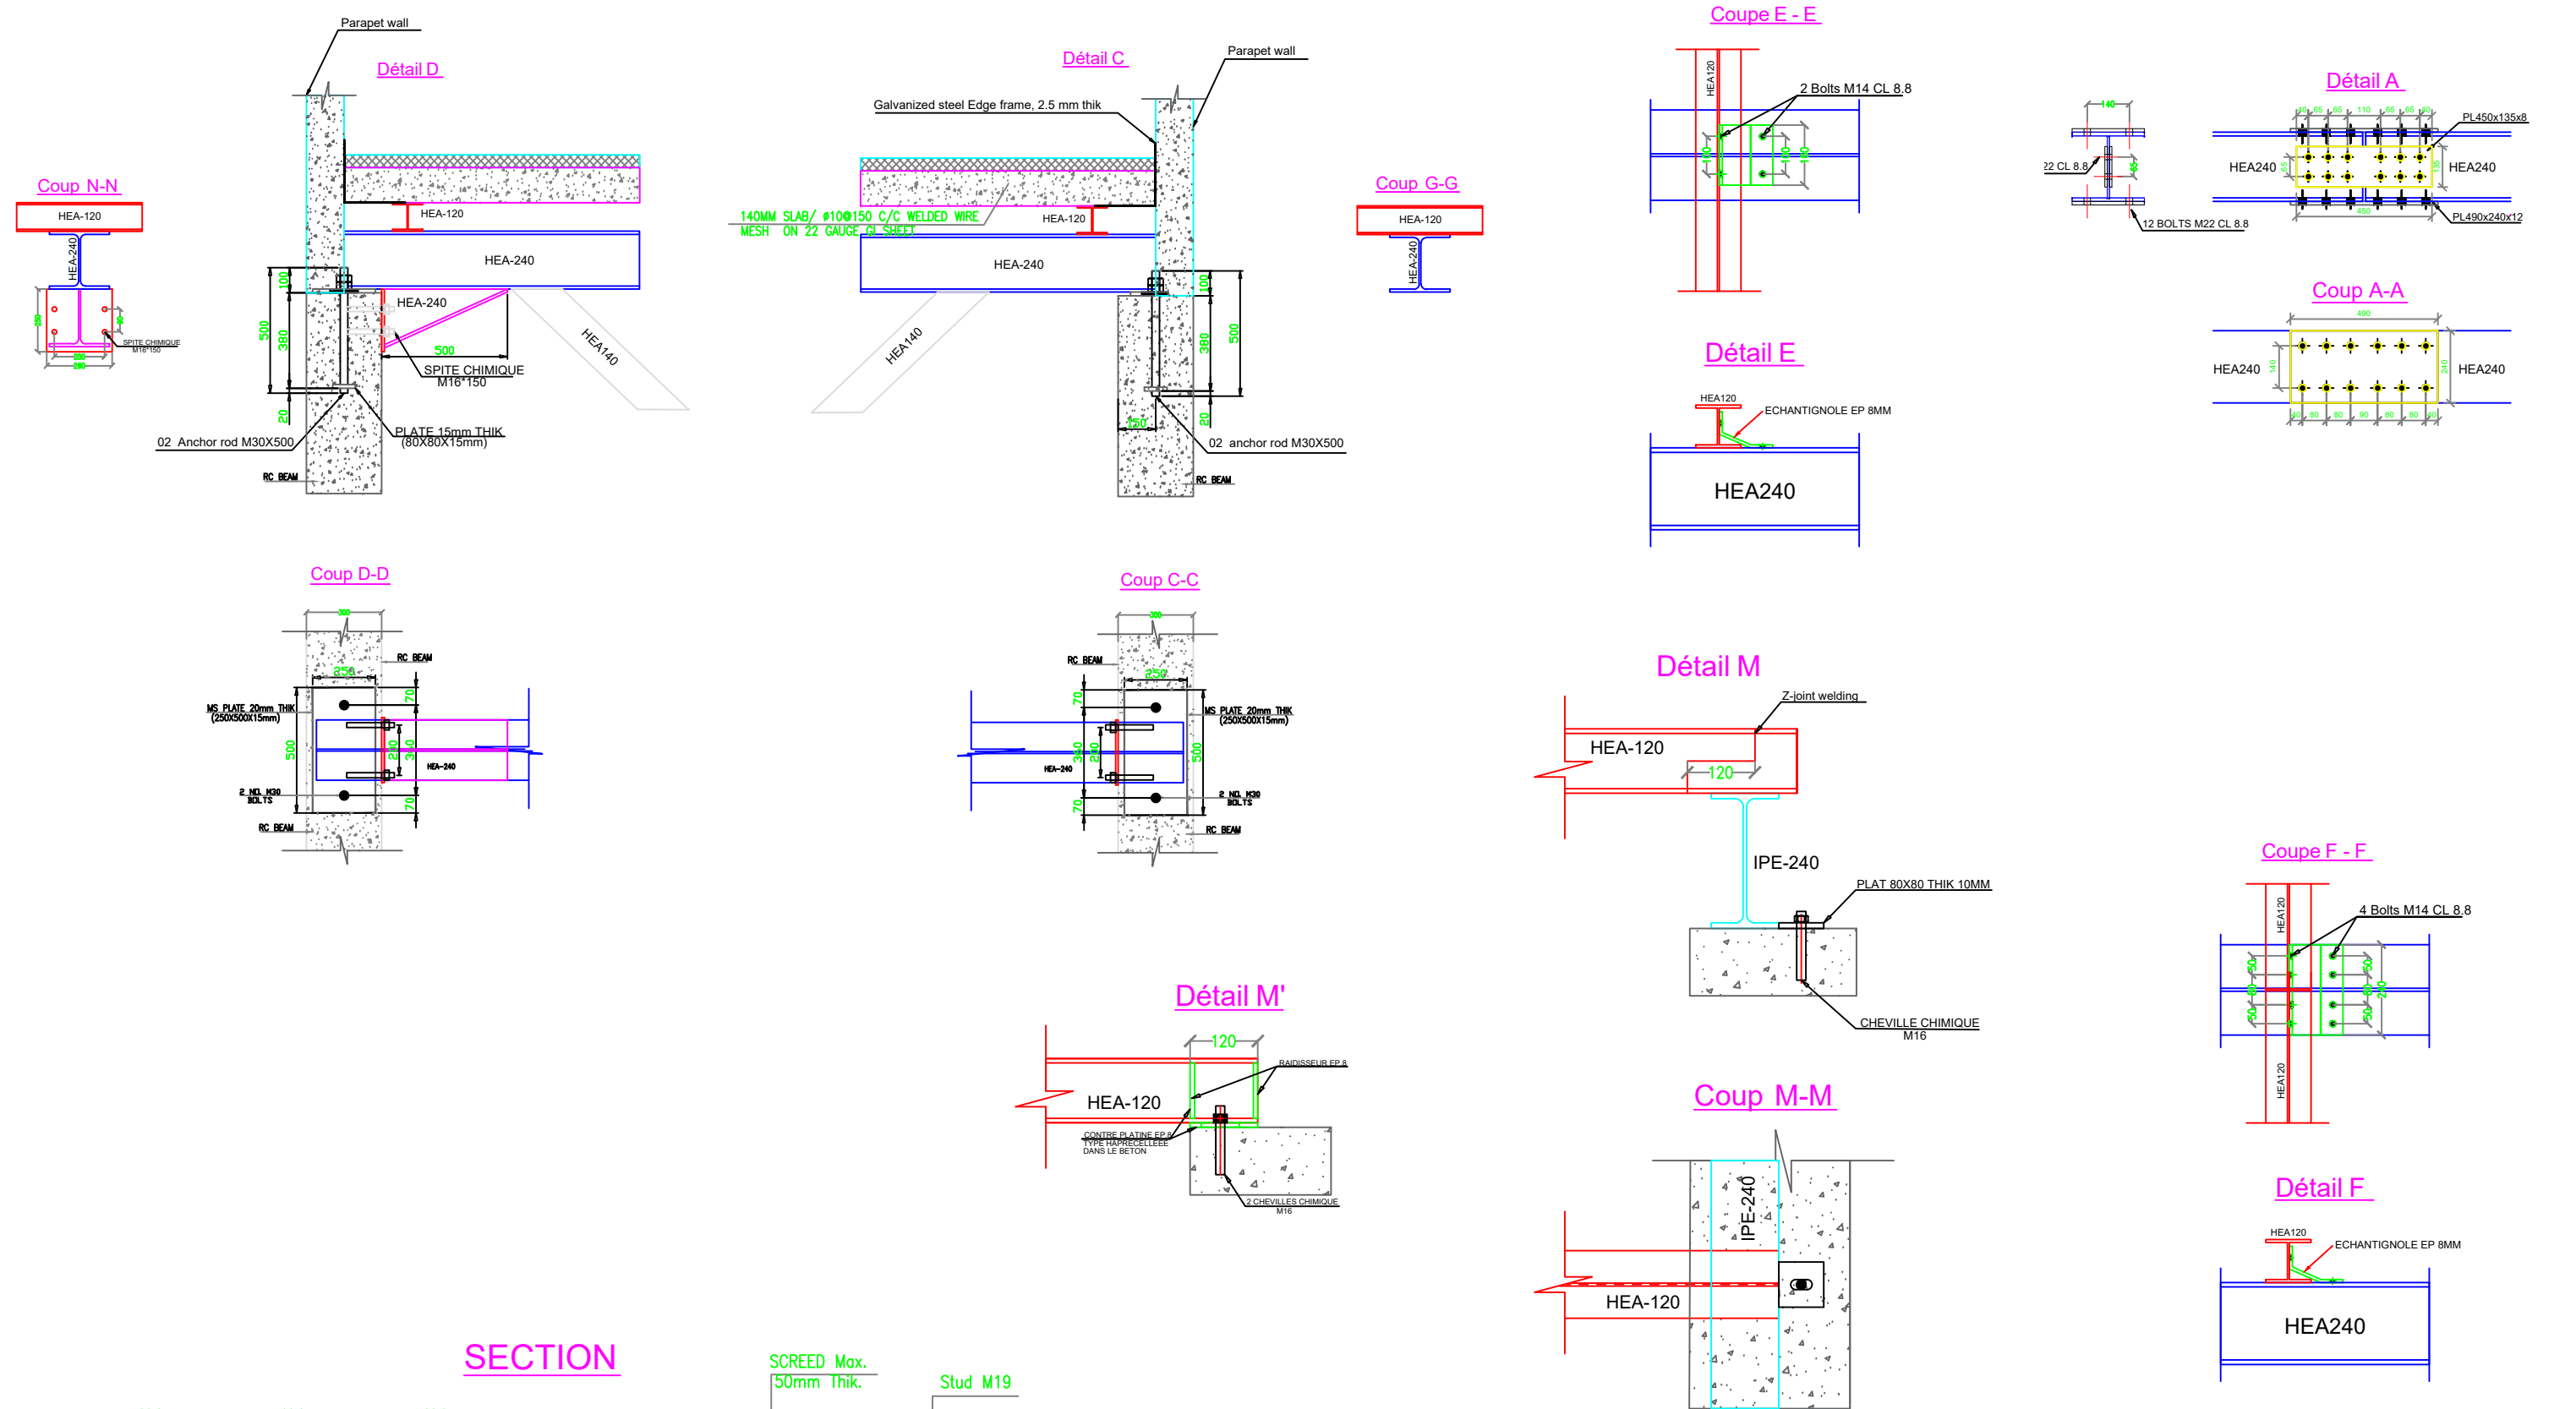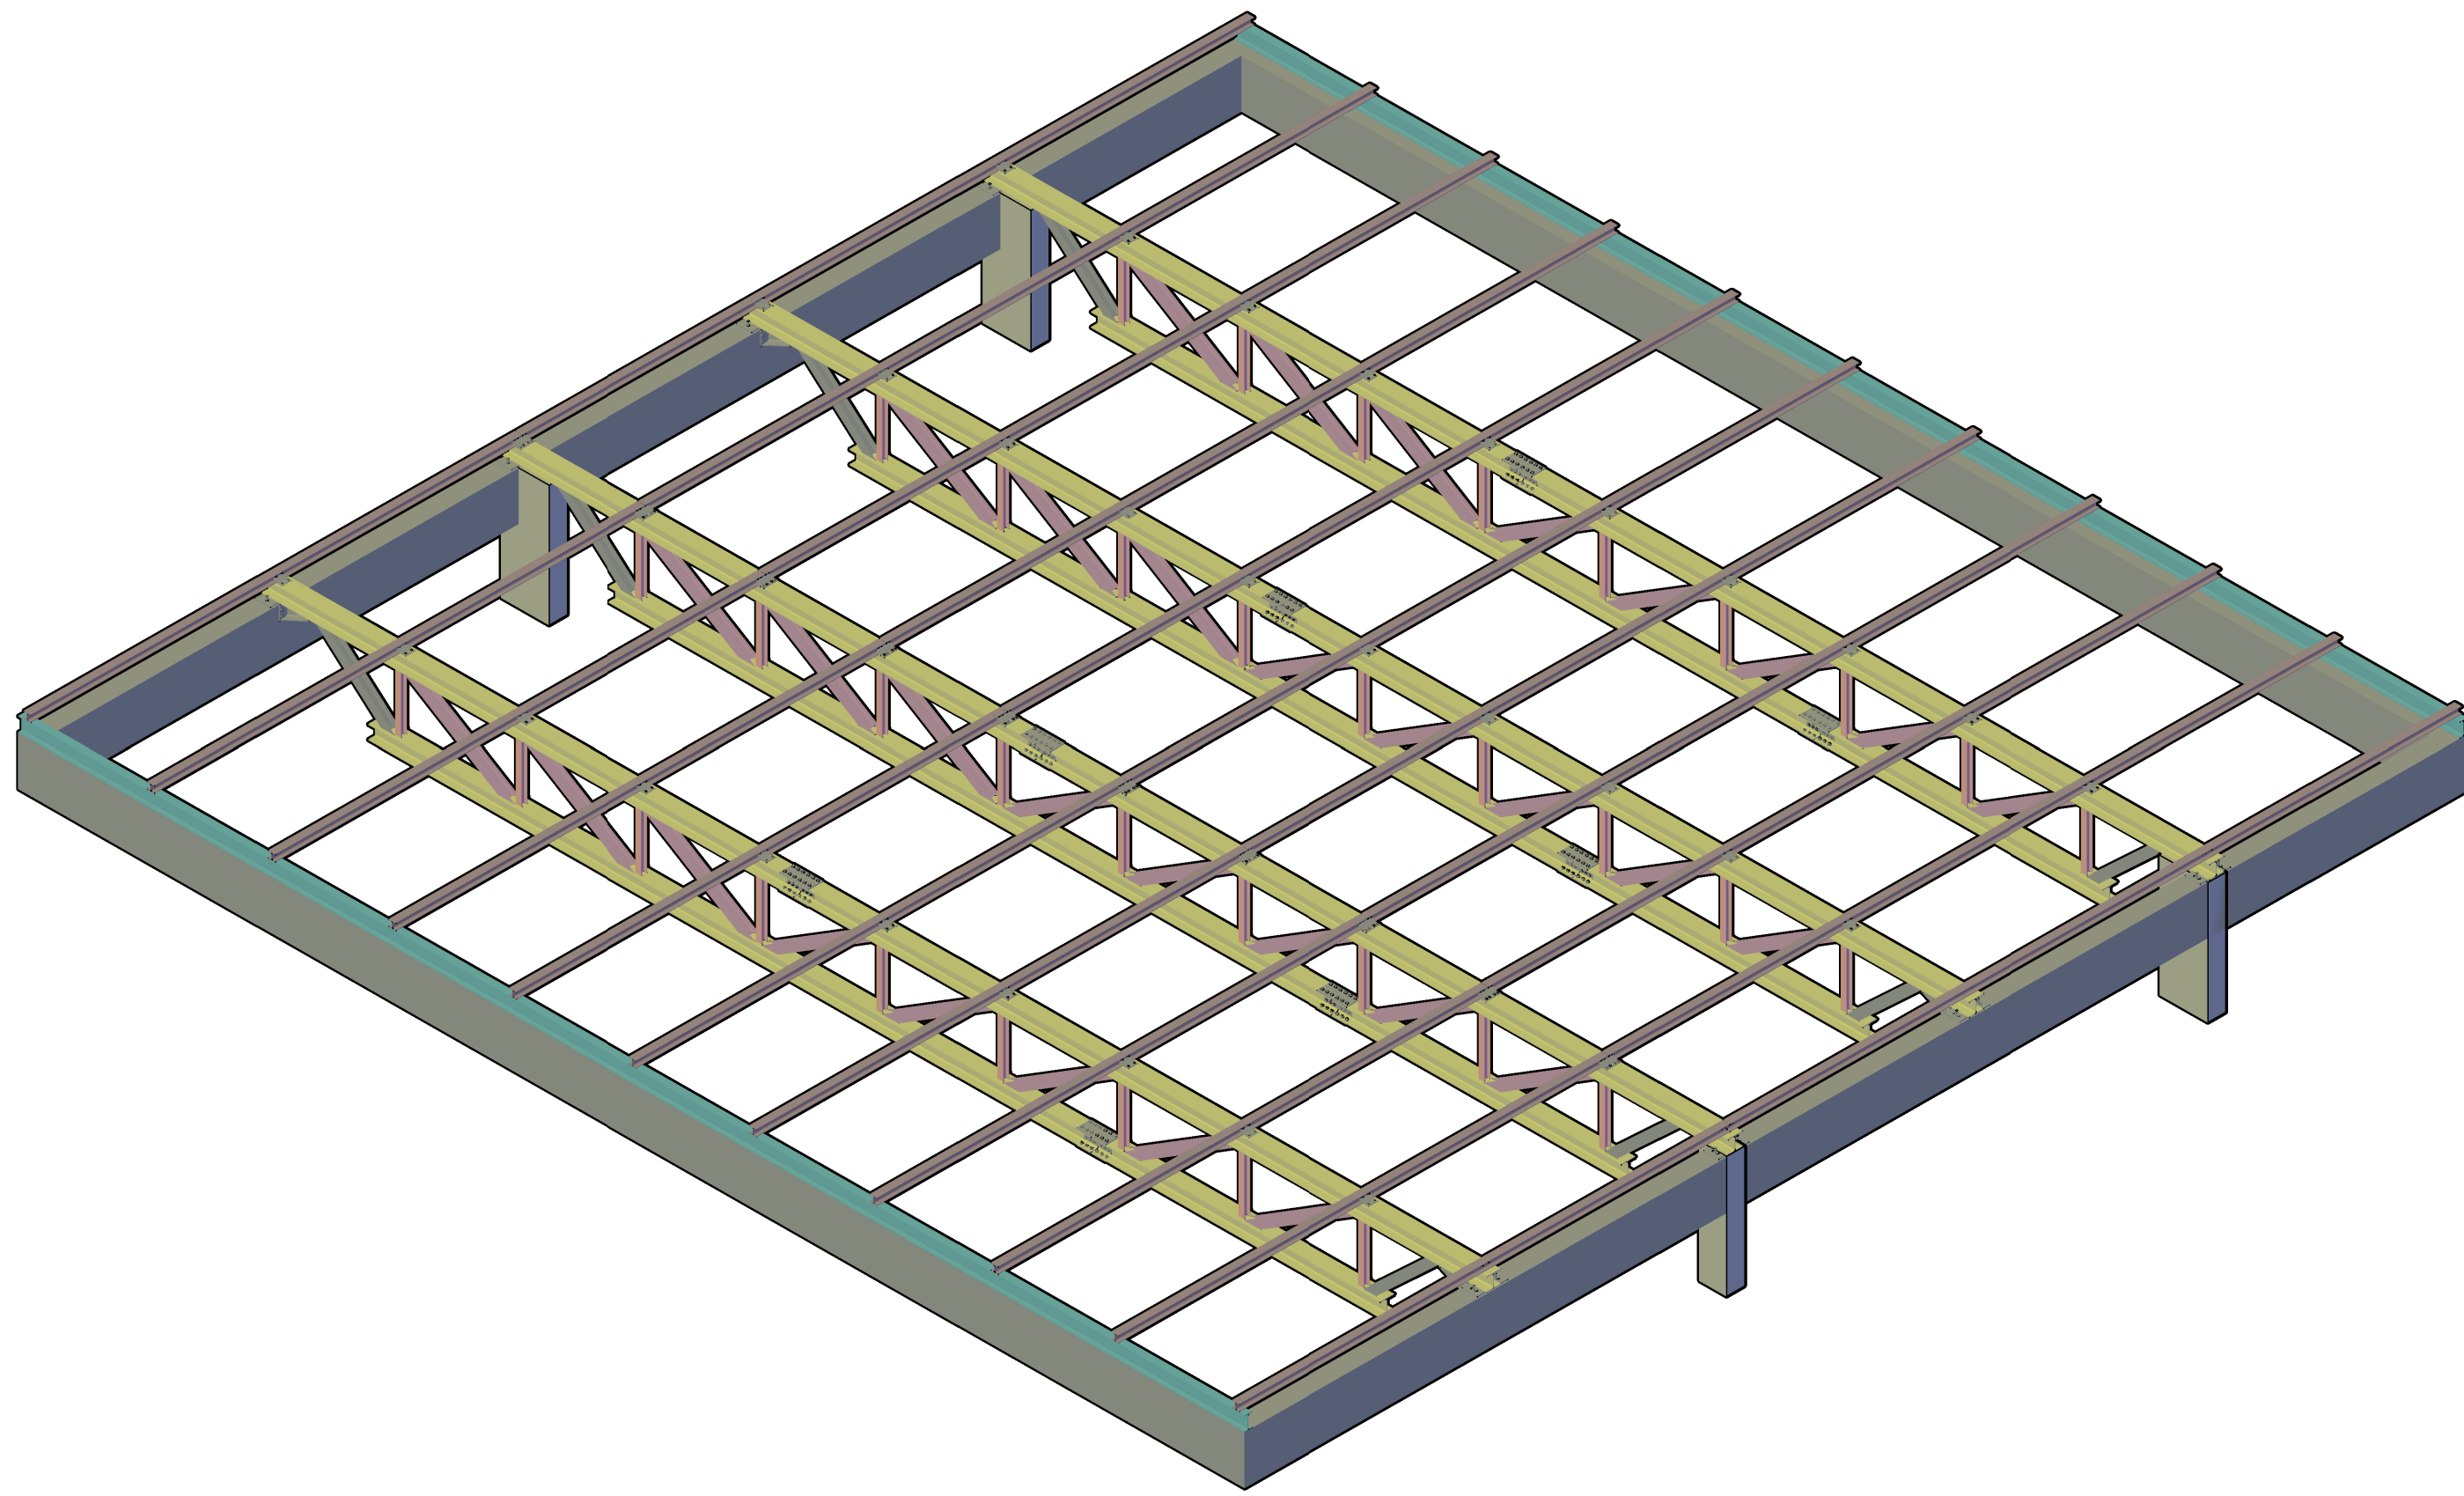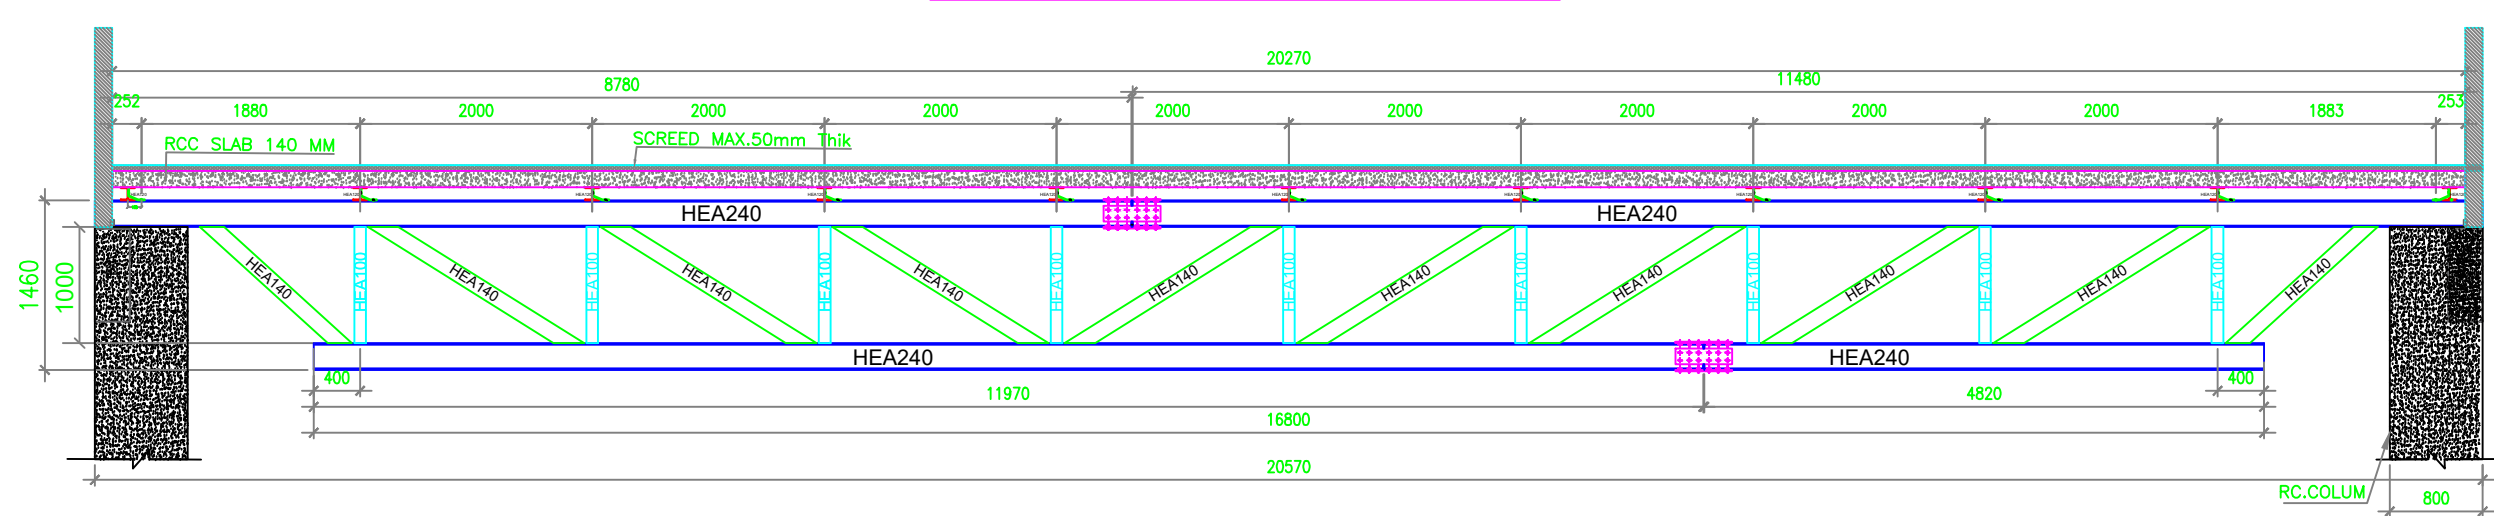

Notes générales: soudure = 0.7 x épaisseur de l'élément le plus mince - sauf indicateur contraire			
Cote fonctionnelle L<= 1m	1m<L<=3m	3m<L<=6m	6m<L<=15m
Tolérance ± 2 mm	± 3 mm	± 4 mm	± 5 mm
15m<L<=25m	25m<L<=40m	40m<L<=60m	L > 60m
± 6 mm	± 7 mm	± 8 mm	± 9 mm
SINERTECH		IHCC	
Administration : Kin. 27, Route Principale 1 Ain el-Helwan Yabilet - Mohammédia		CLIENT: IHCC	
Date: 13/10/2025		TITRE : UPPER ROOF TOP STRUCTURE HOSPITAL ZNATA	
Dessiné par : LAZIZ		Vérifié par : ET EL MOURAD	
Approuvé par : SOCOTEC		DESIGNATION : DR-ST-HZ	
Echelles :		Ce plan est la propriété de SINERTECH Industrie et ne peut être reproduit ou communiqué sans son autorisation. This drawing belongs to the SINERTECH Industrie and cannot be duplicated or communicated without its permission.	