
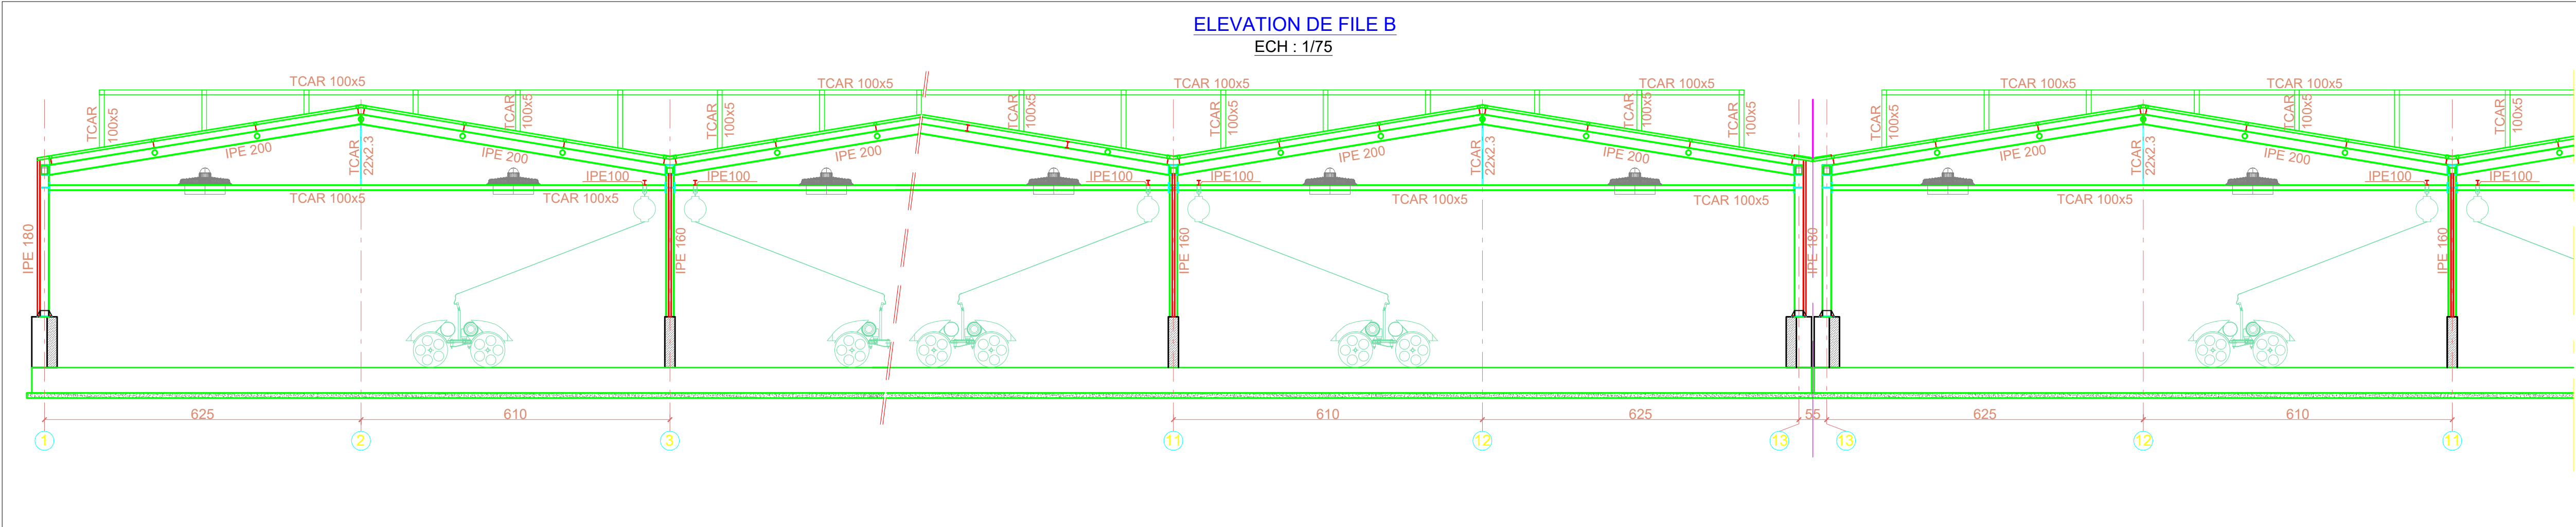
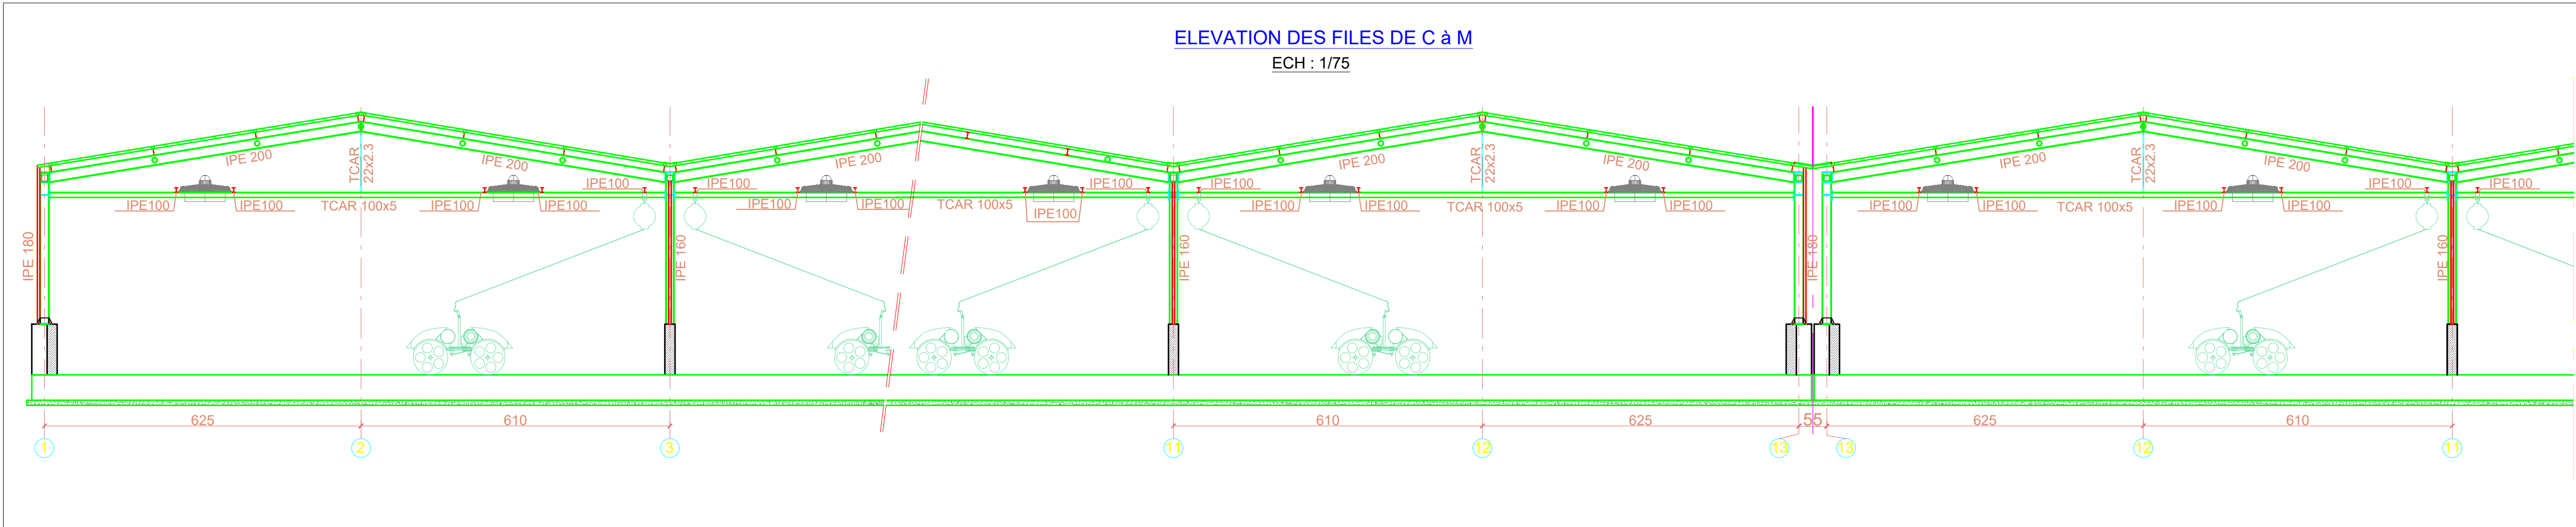
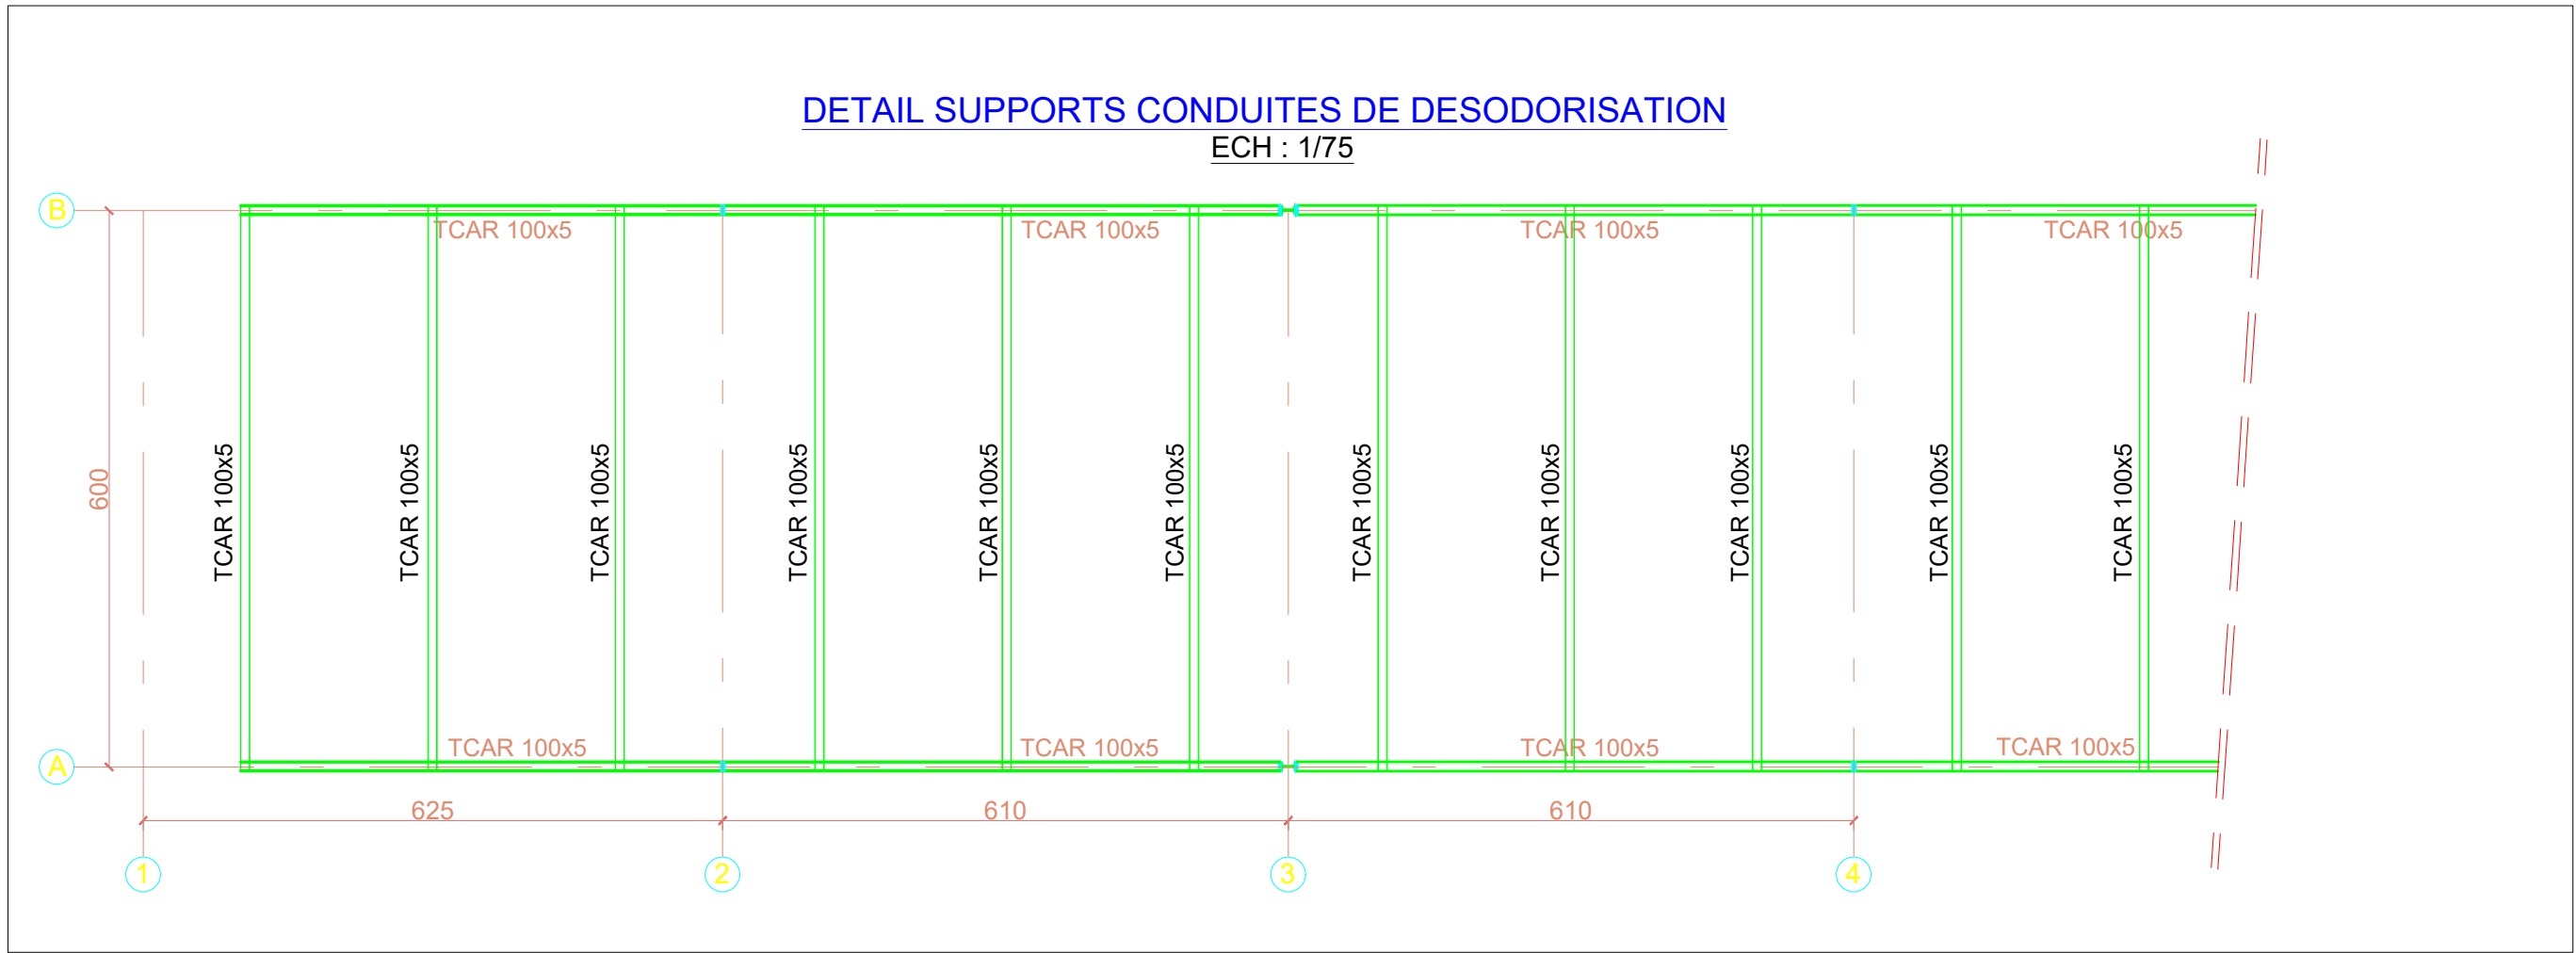
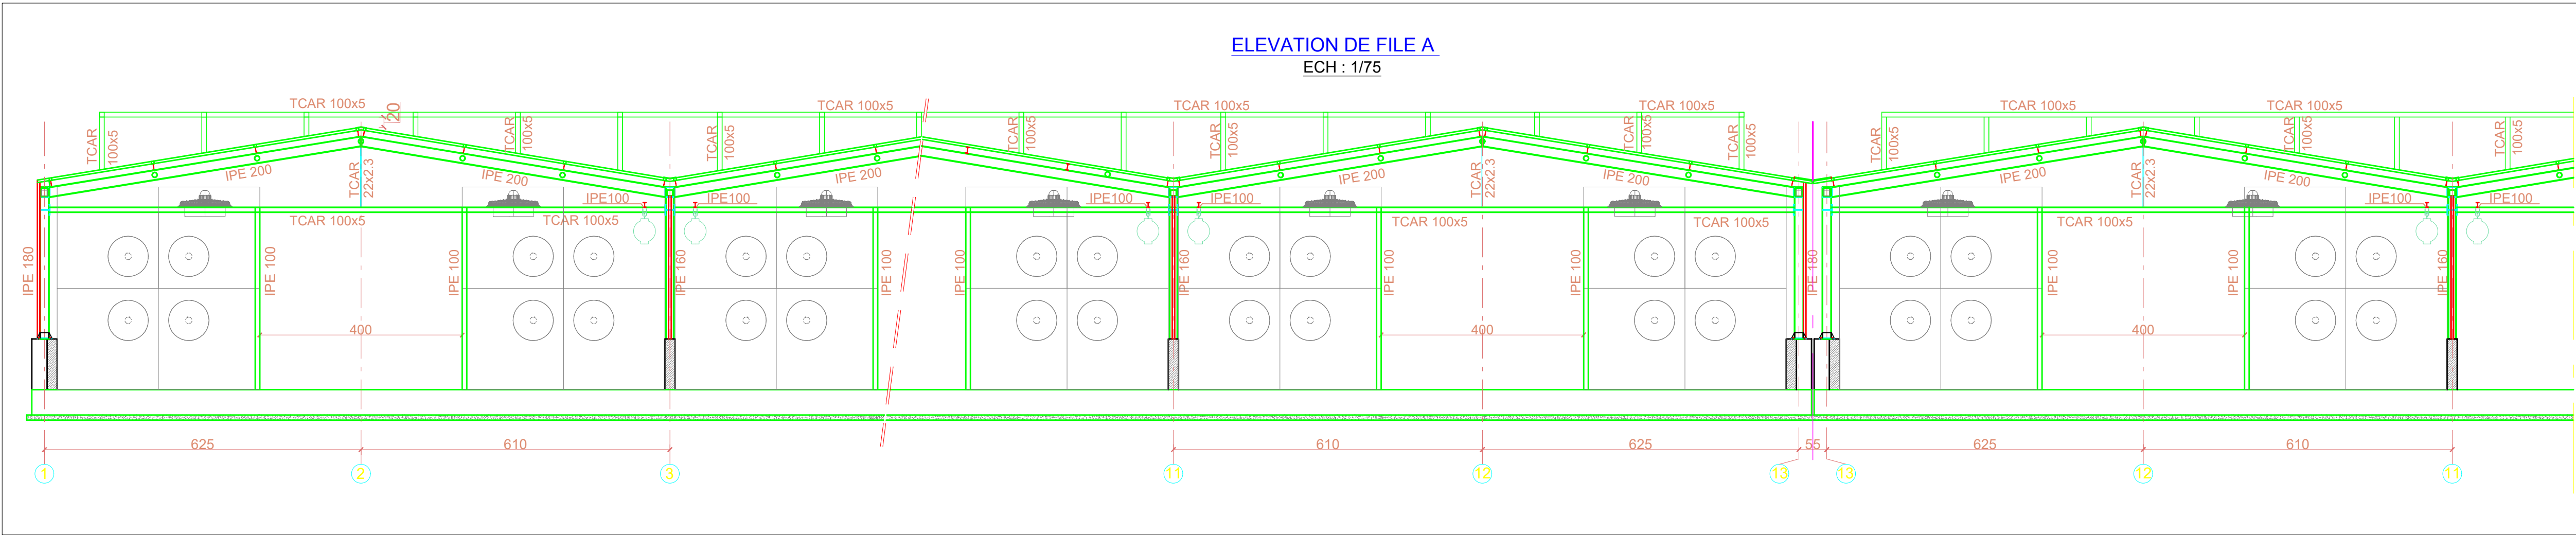
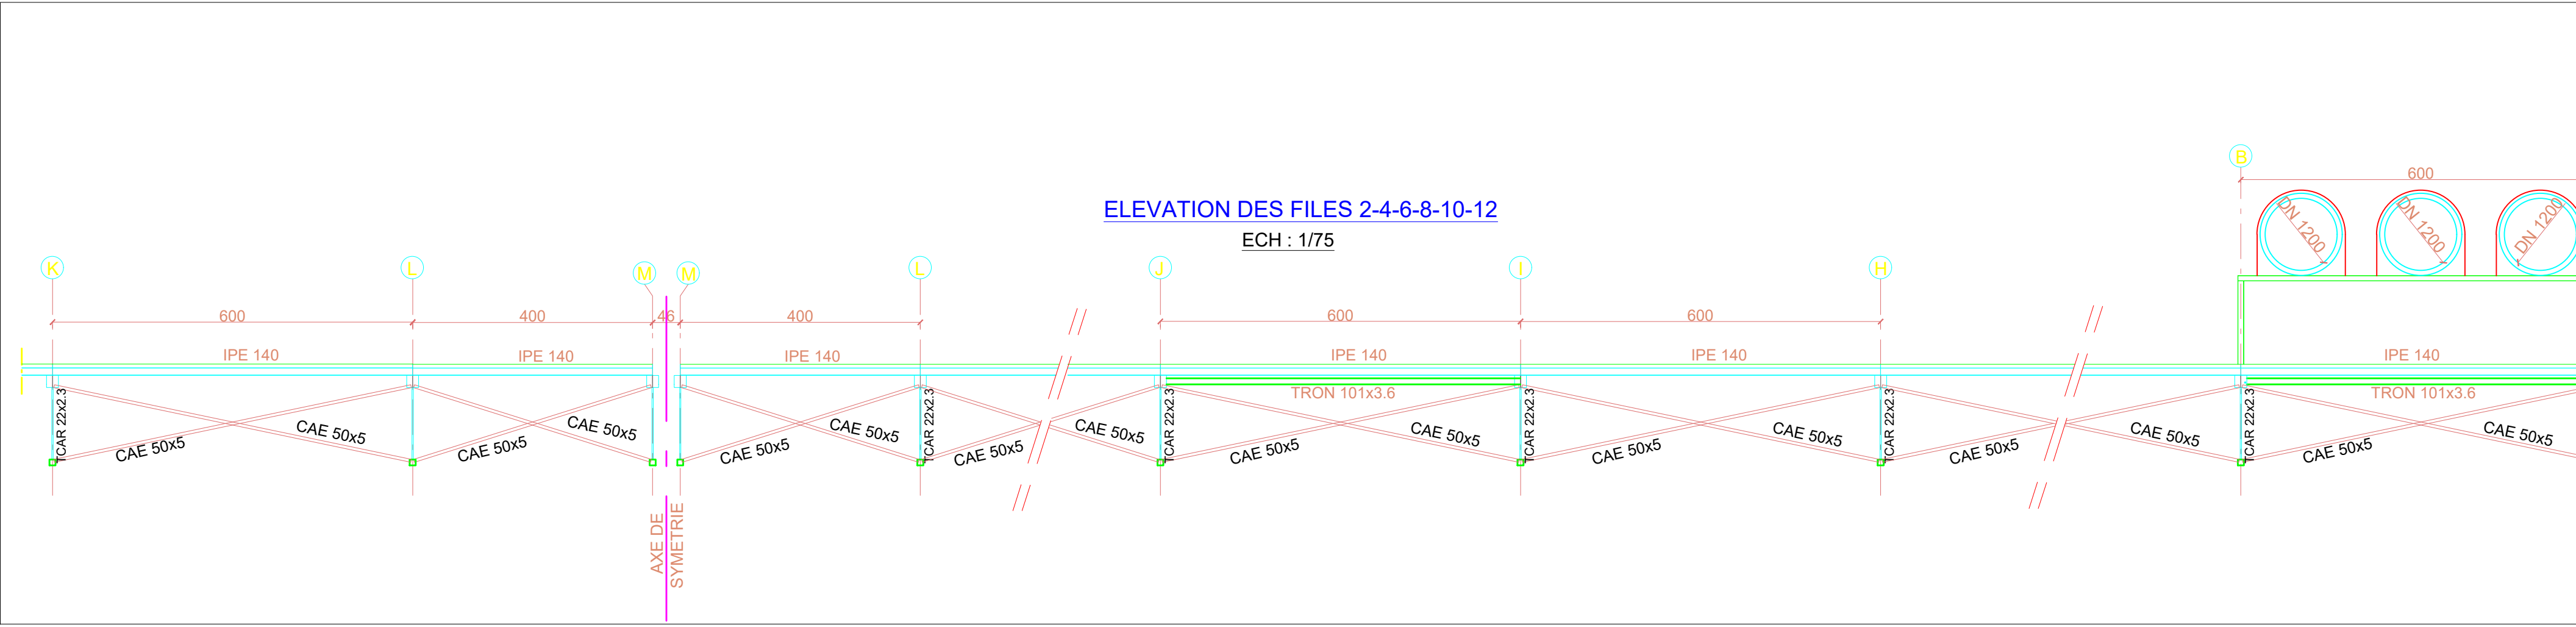
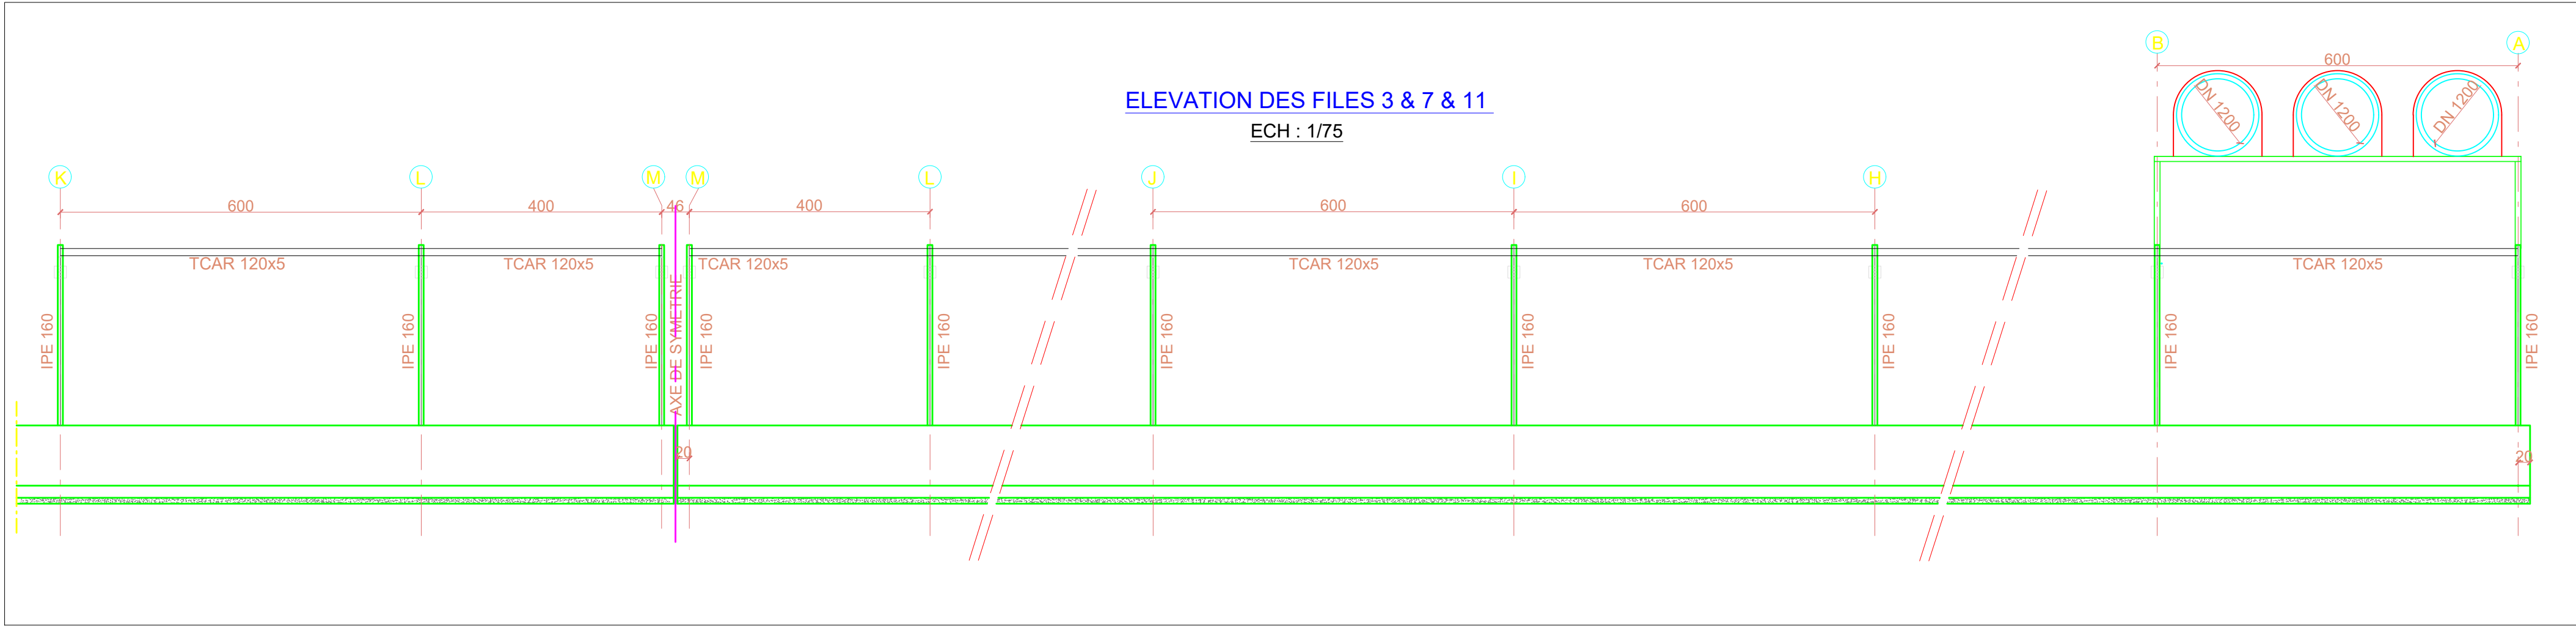
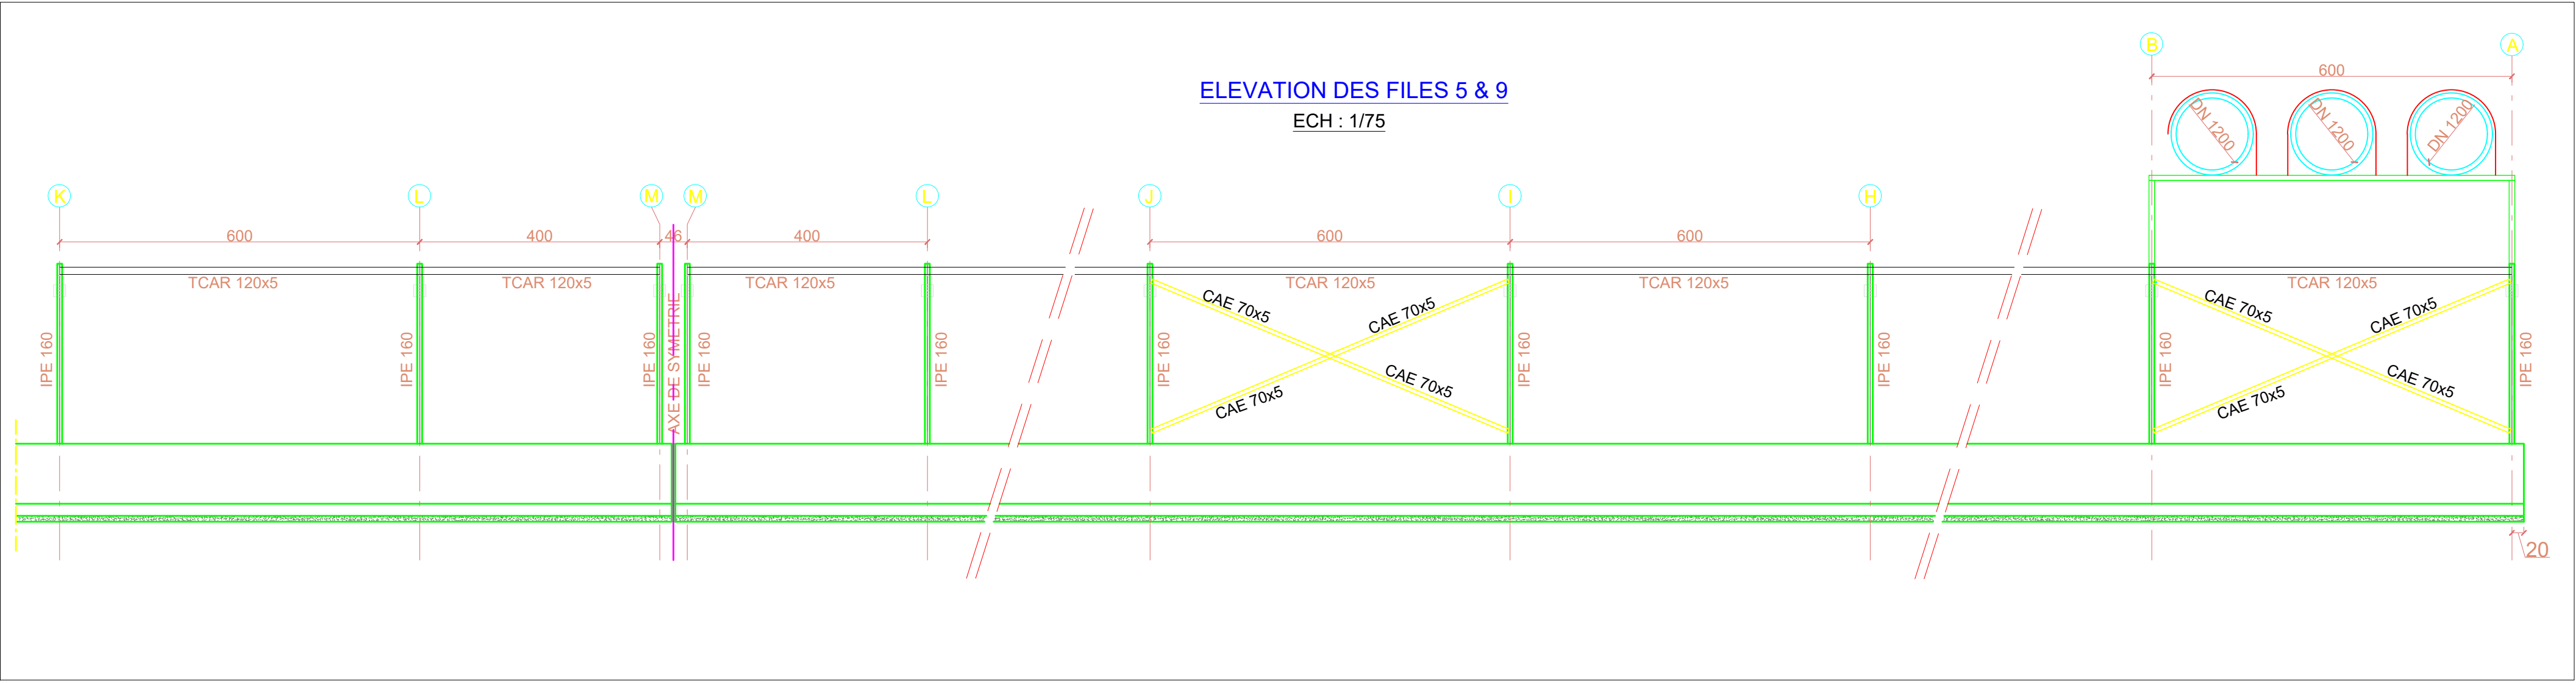


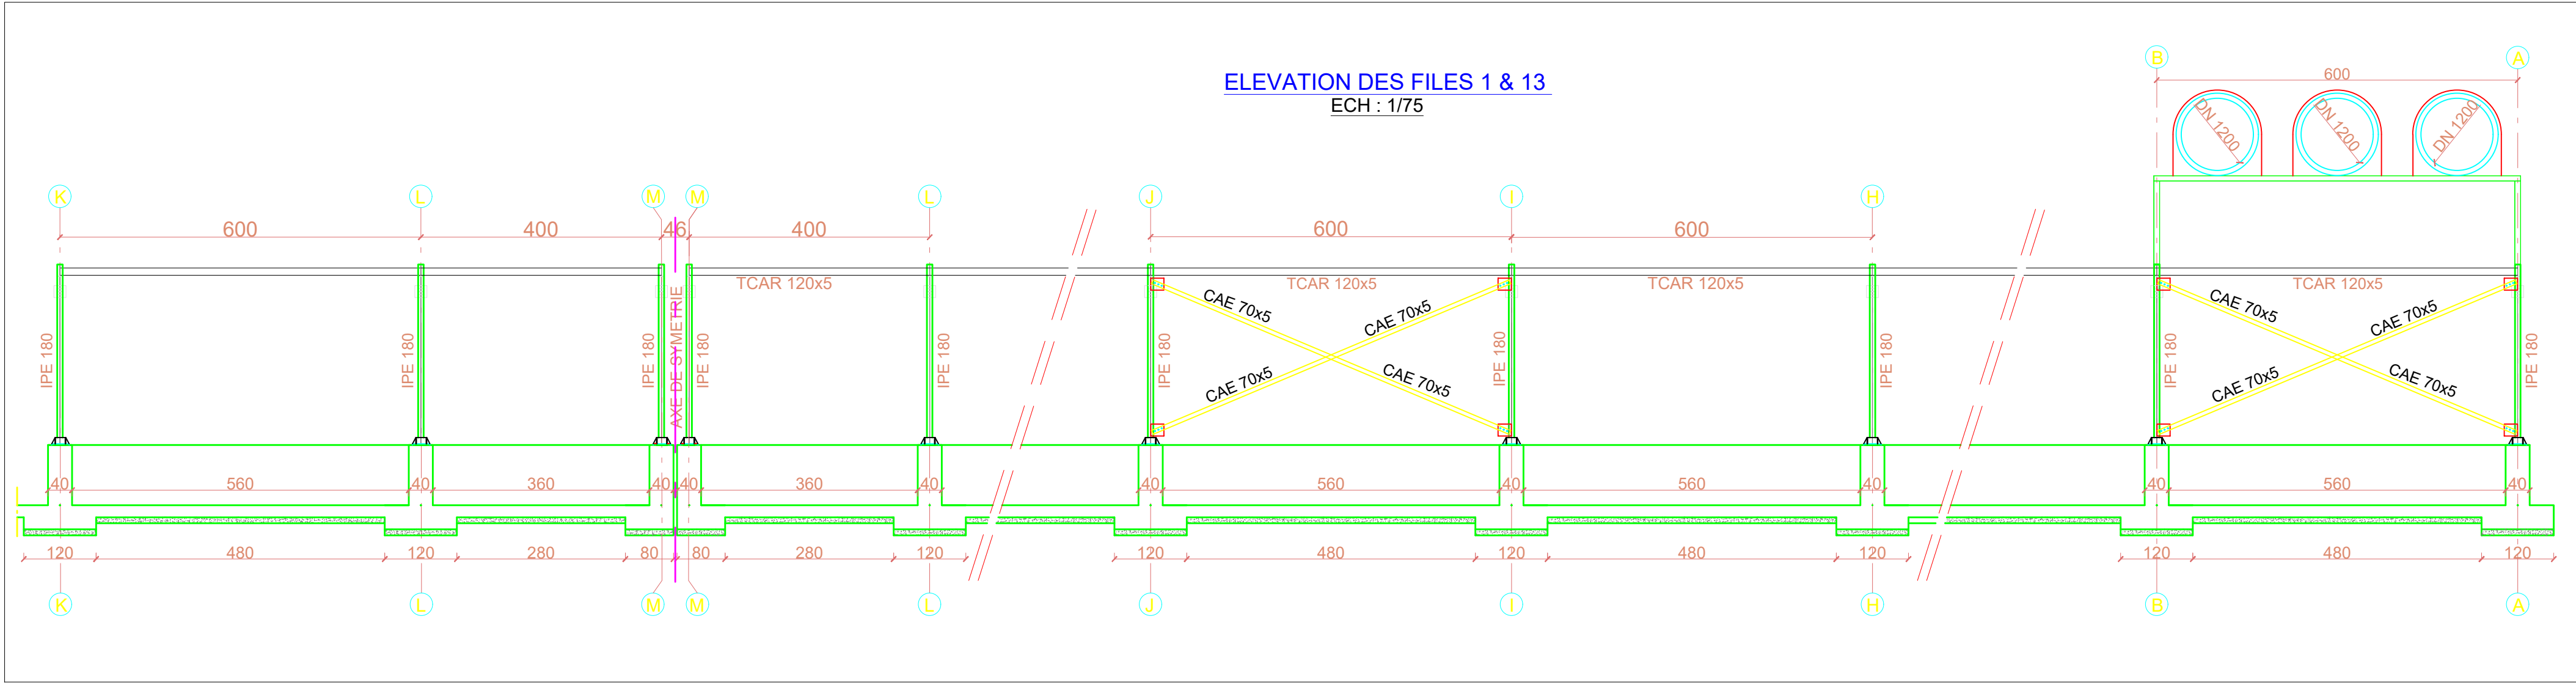

Nota:

- Acier E28 pour les profils
- Acier E24 pour les platines
- Epaisseur soudure = 0,7xc
- c = Epaisseur de l'élément à souder
- Boulons classe 8.8
- Tiges d'ancrage classe 8.8

N.B:

- Toutes les pannes sont en IPE 140
- Toutes les lécres sont en Ø16
- Toutes les diagonales des pâtes de stabilité sont en cornière L70x7
- Toutes les diagonales de la couverture sont en cornière L50x5

ROYAUME DU MAROC

REGIE AUTONOME MULTI-SERVICES D'AGADIR

الوكالة المستقلة
RAMSA

TRAVAUX DE MISE A NIVEAU EXTENSION
ET L'EXPLOITATION DE LA STEP MZAR

-PLAN CHARPENTE METALLIQUE-
-COUPES-

Echelles : 1/75	Code ouvrage : PLAN D'EXECUTION	PLAN N°: SINC STIP OM 0817	Indice A
C			
B			
A	23/02/2024	Première édition	
Indice	Date	Modifications	Visa
INTERVENANTS	Nom	VISA	DATE
DESSINATEUR/PROJETEUR			
Ingénieur GC de structure			
VERIFICATEUR			