


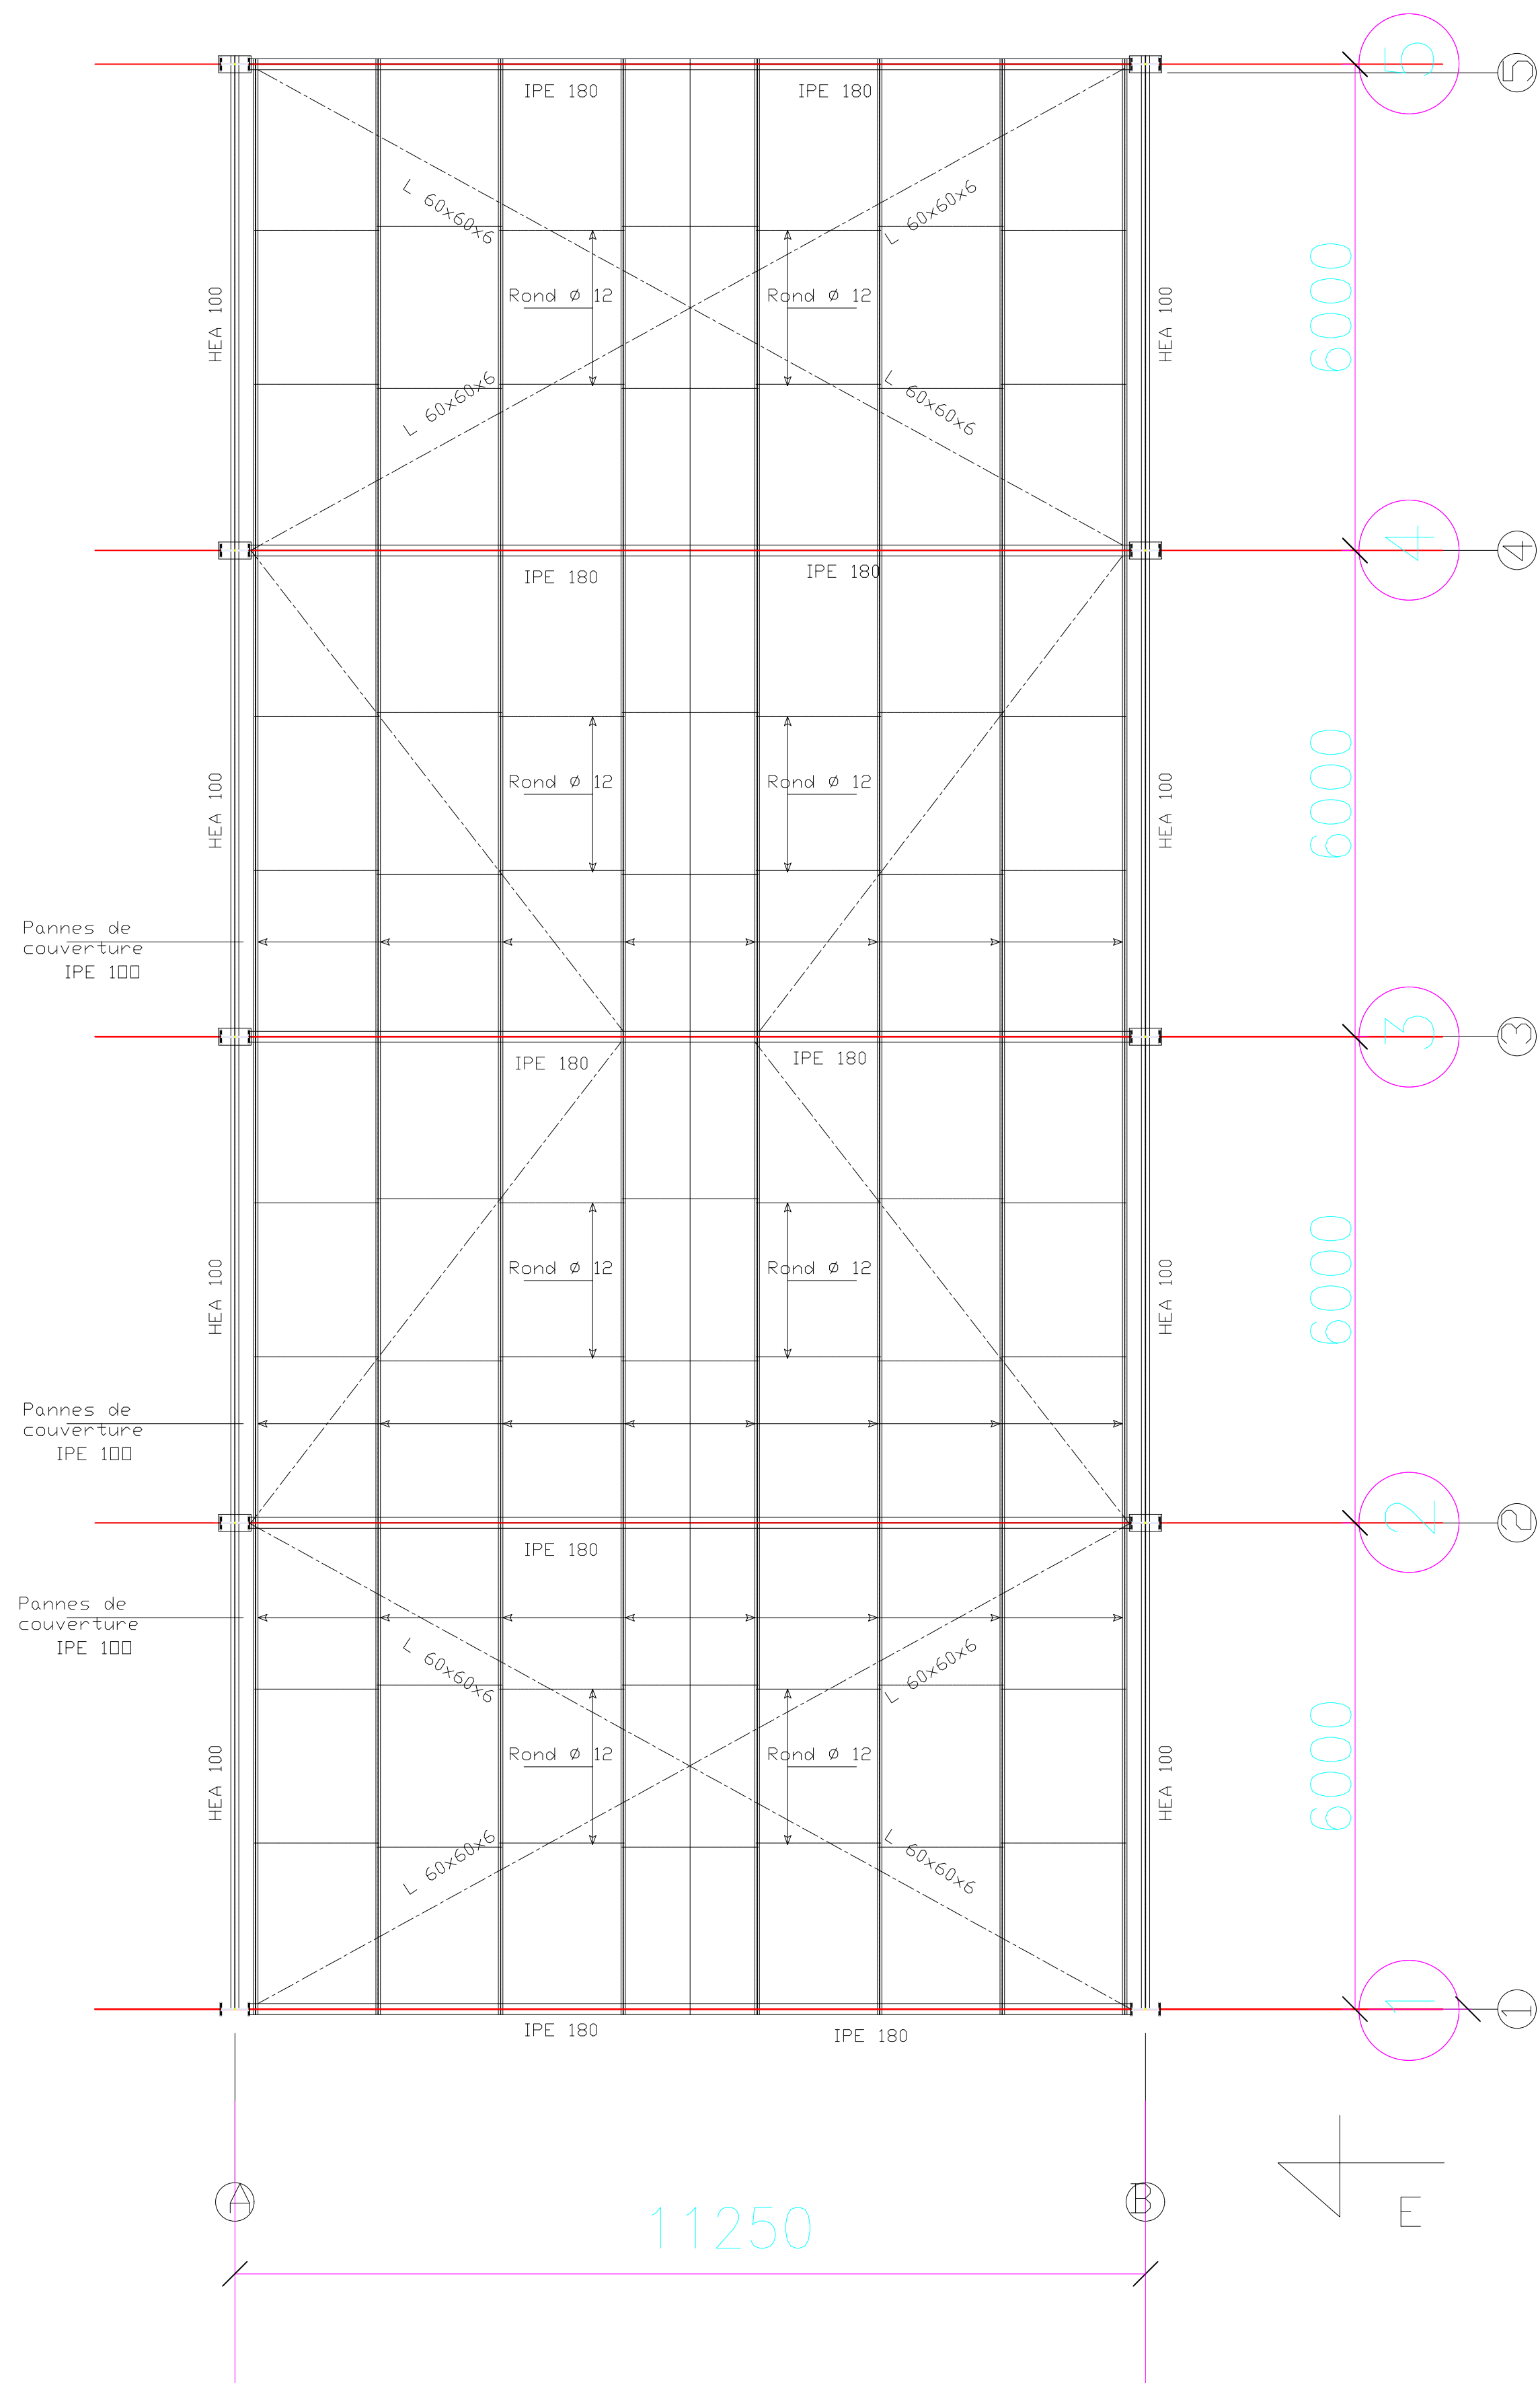
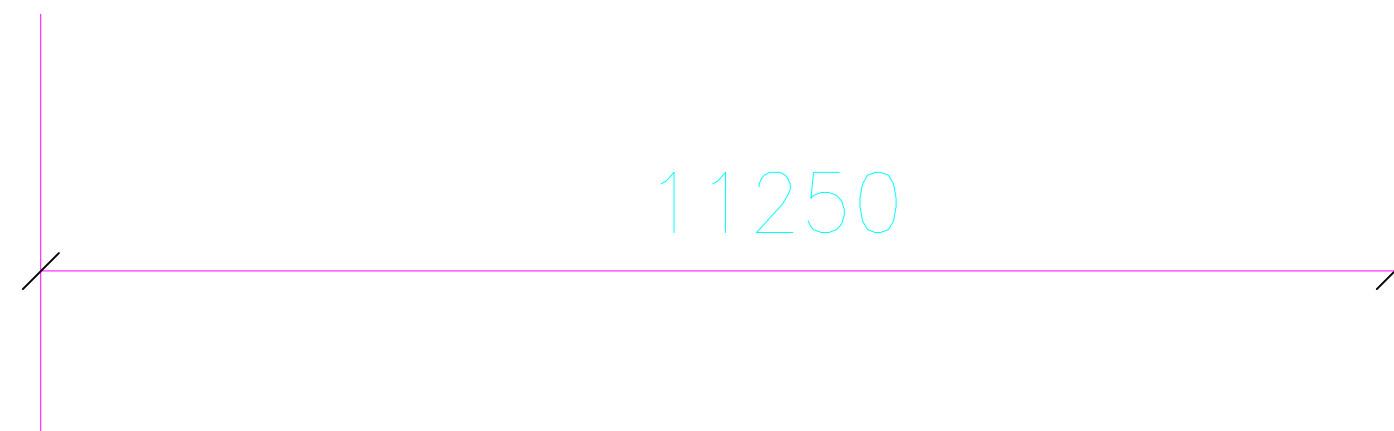


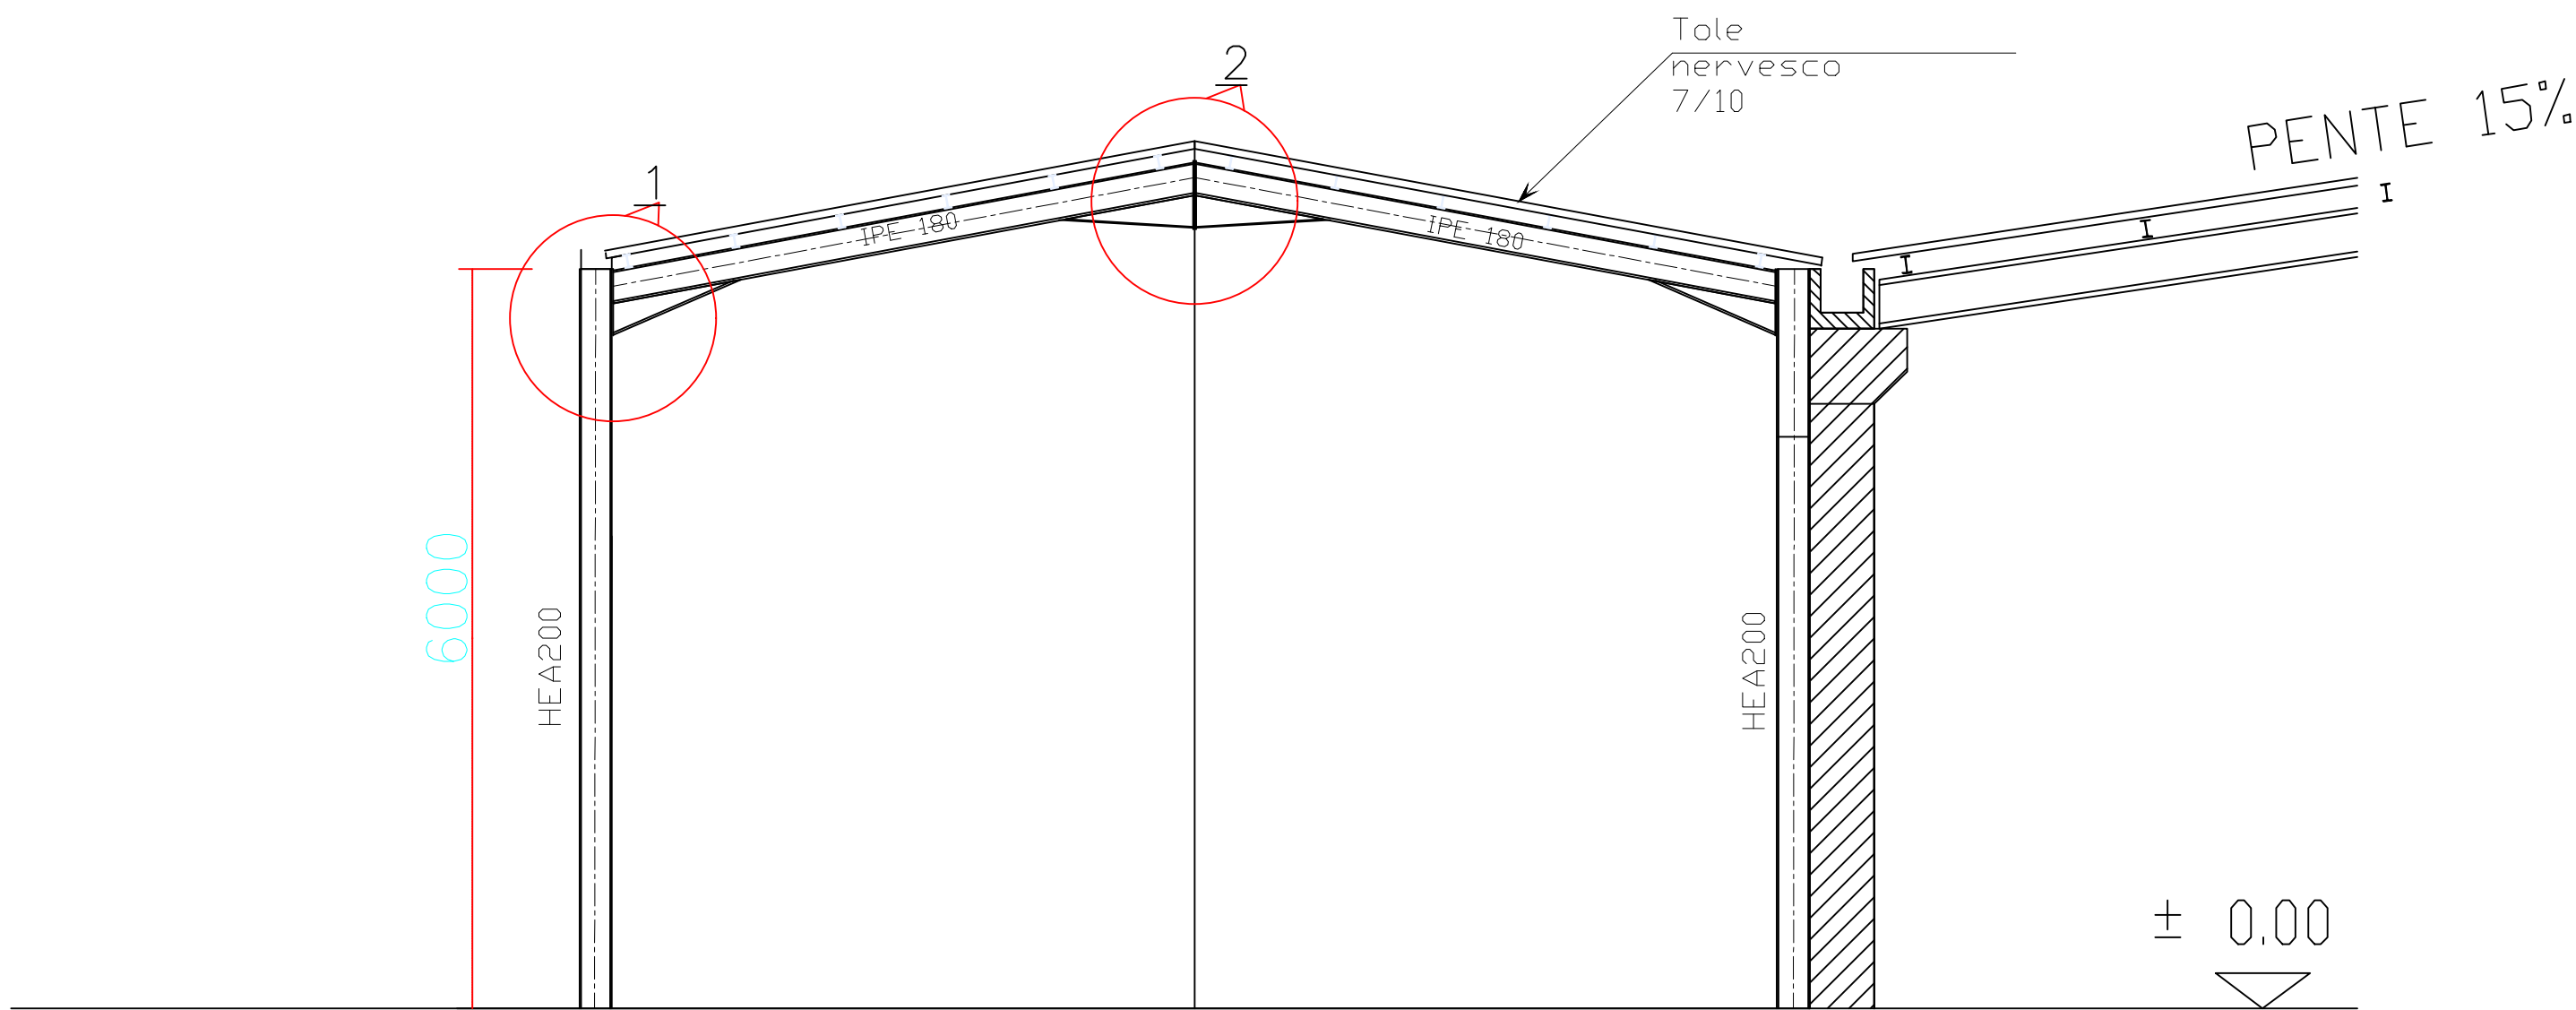


VUE
FAÇADE LATÉRALE GAUCHE

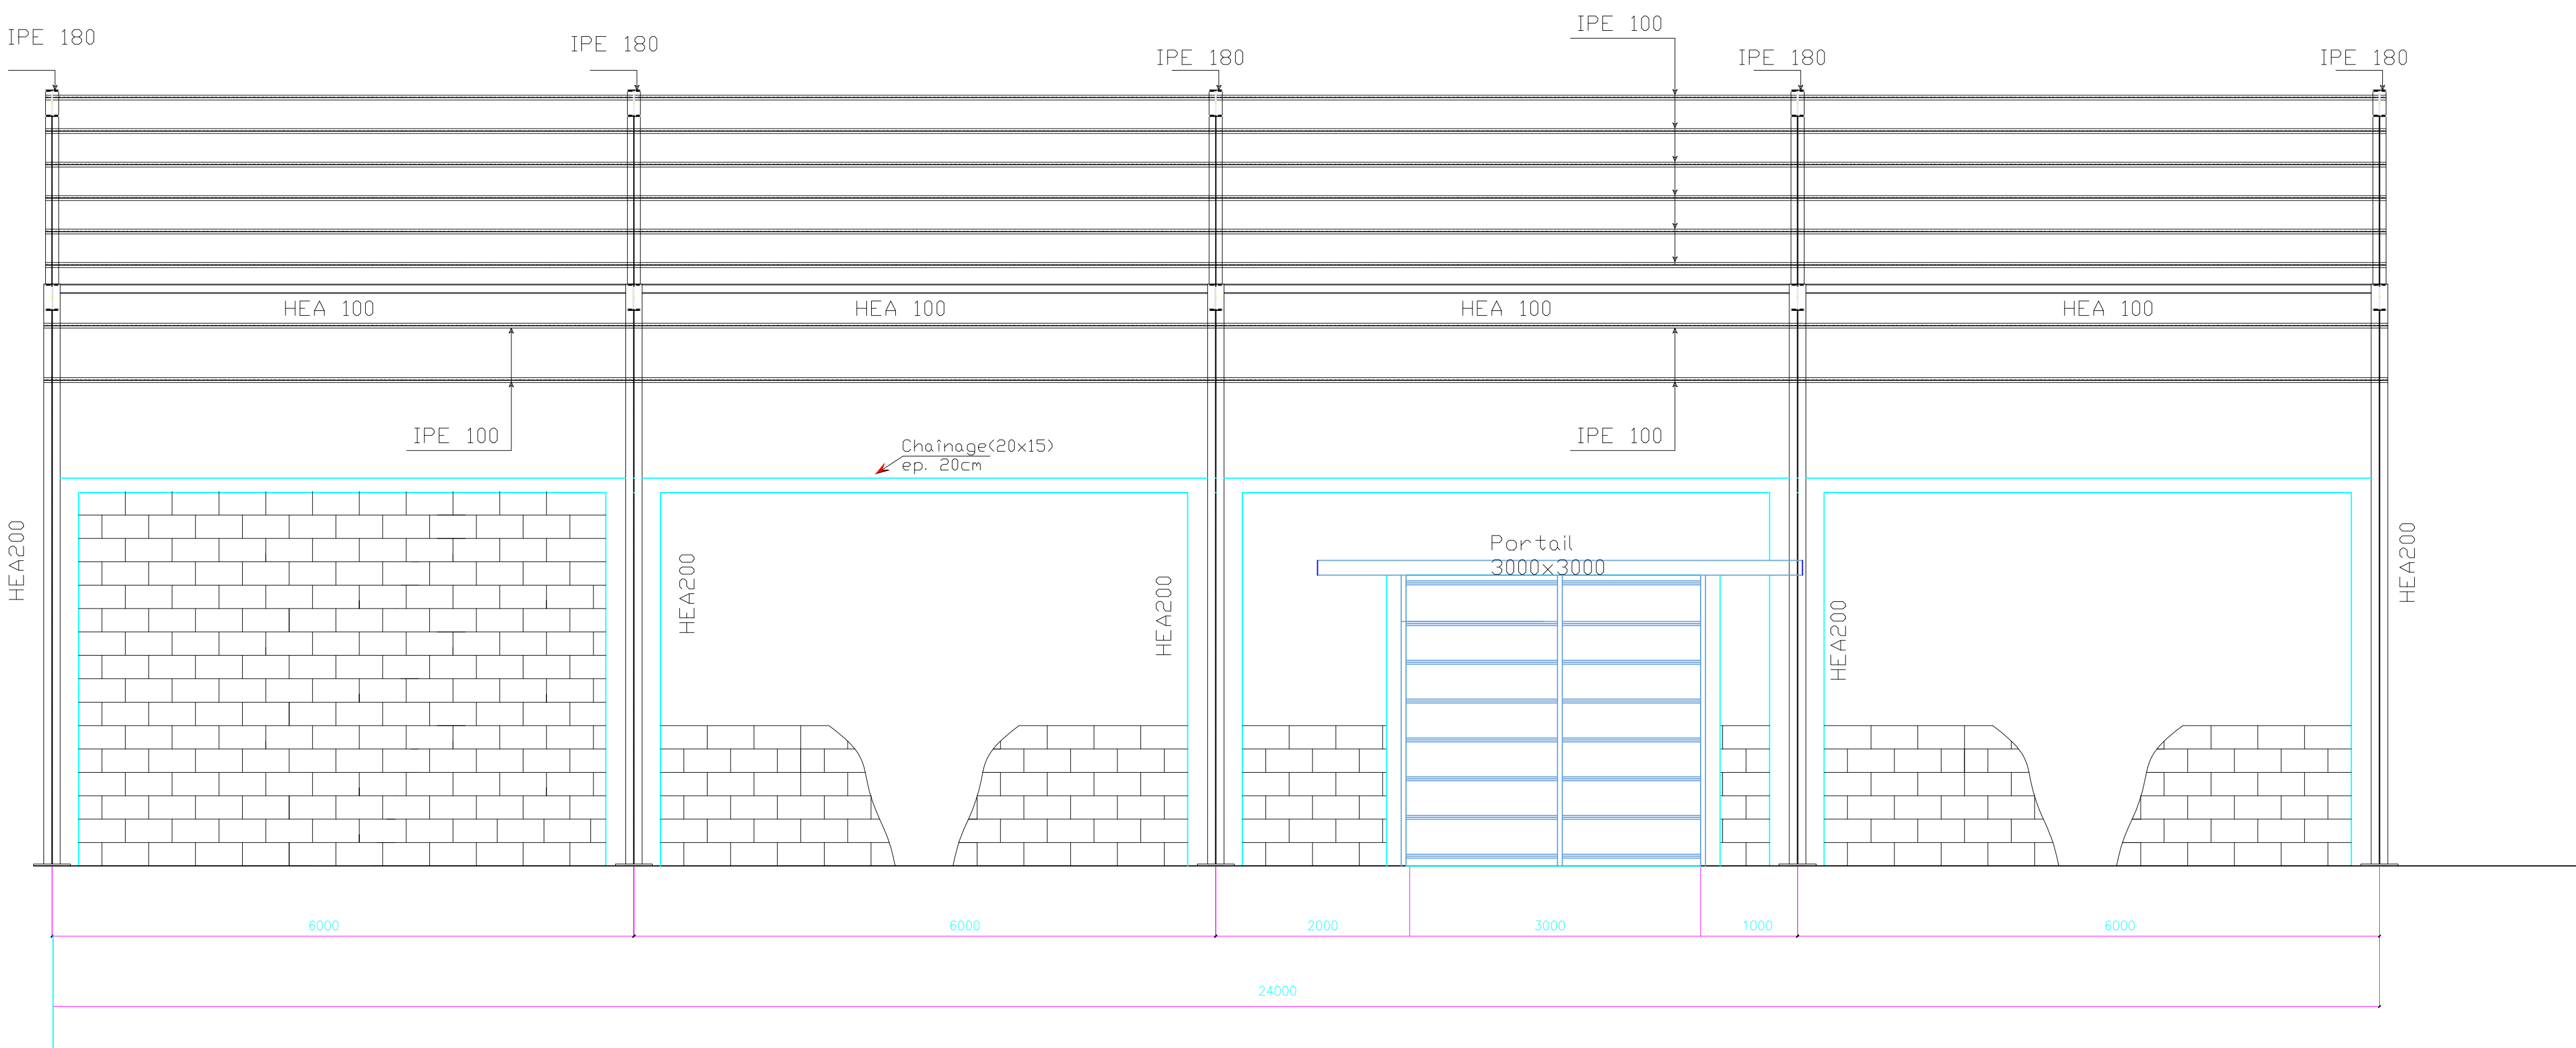


DETAIL: 1

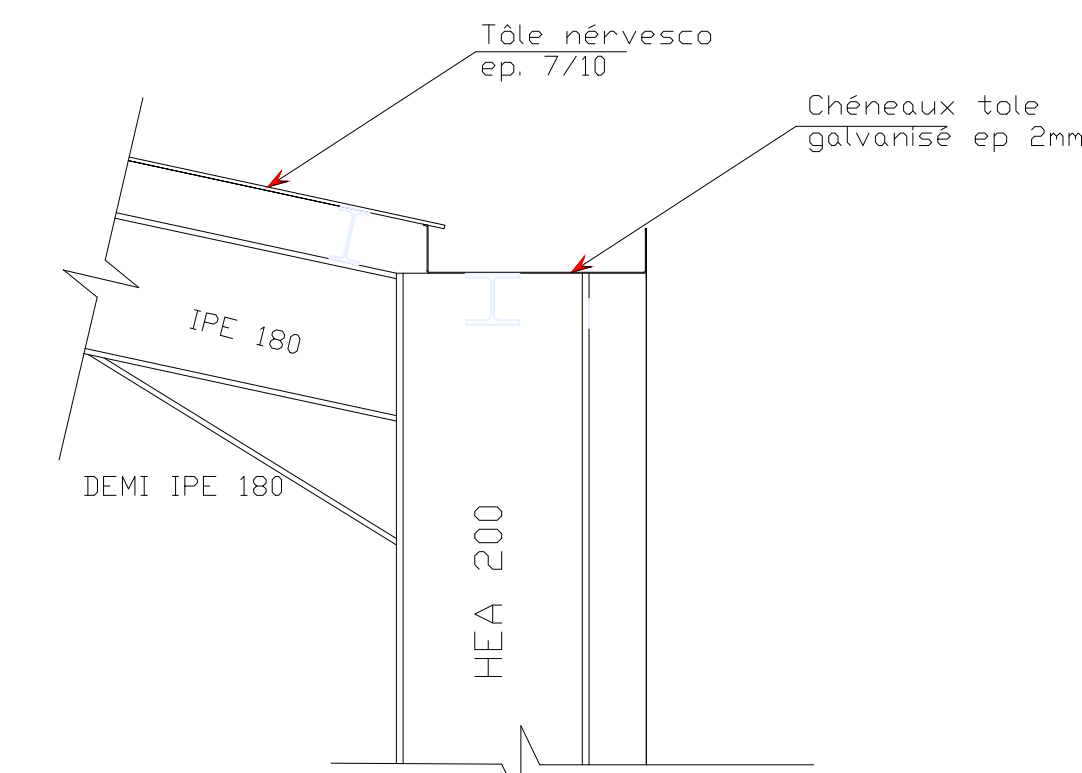


DETAIL: 2

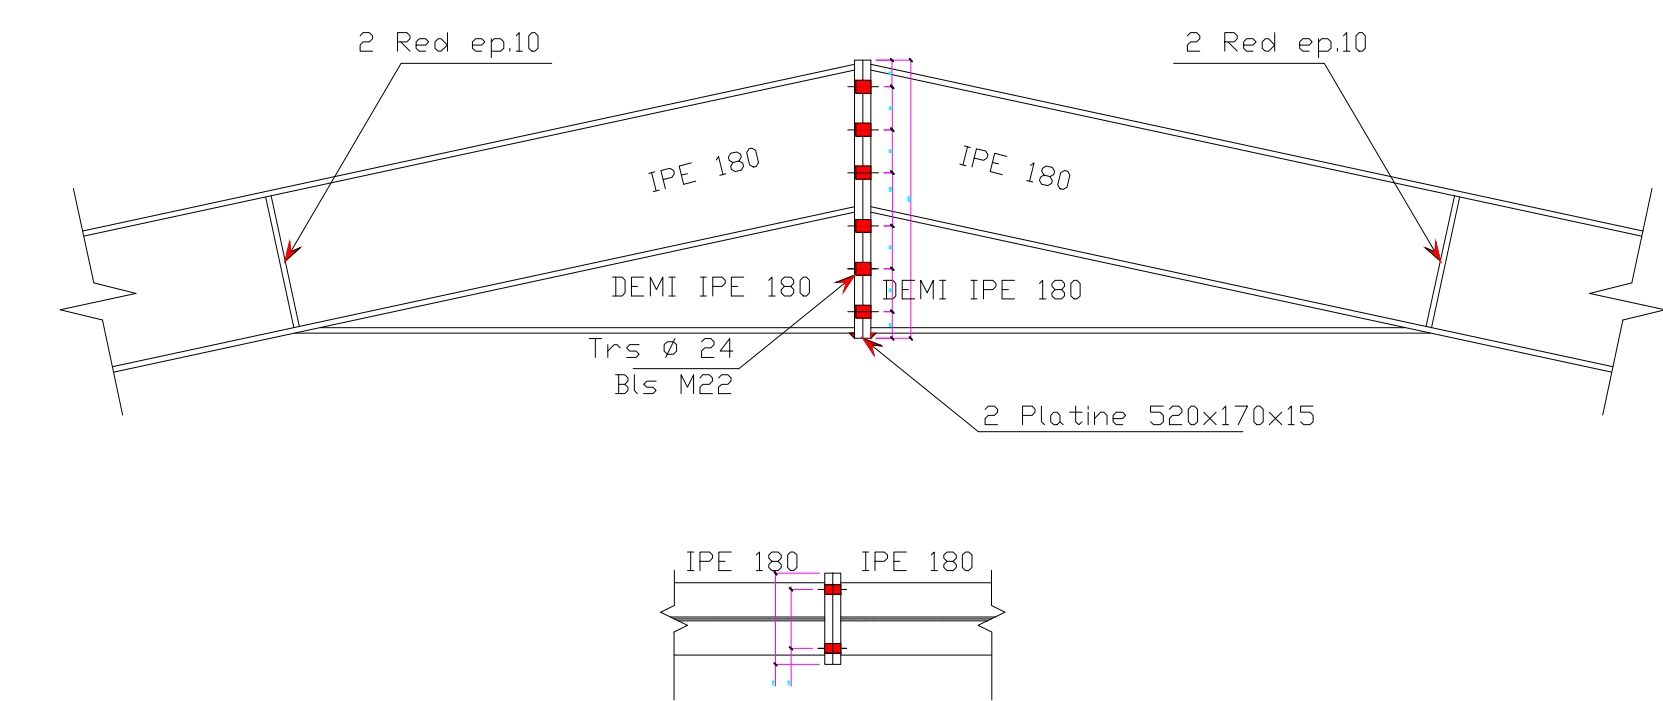


DETAIL: 3

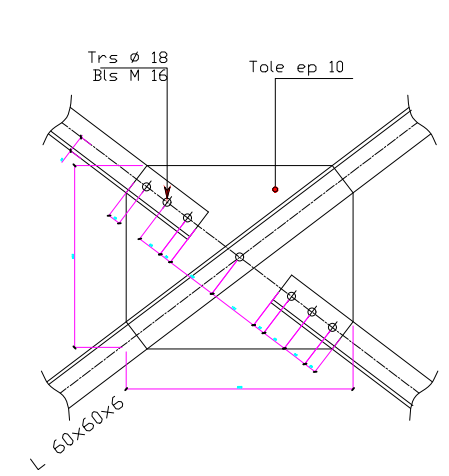


DETAIL: 4

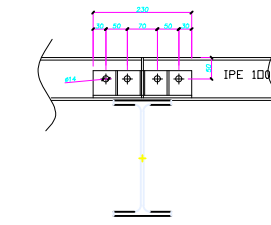

DETAIL: 5

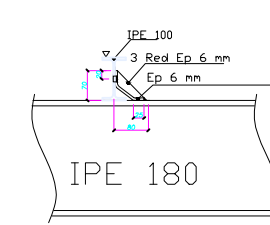

DETAIL: 6

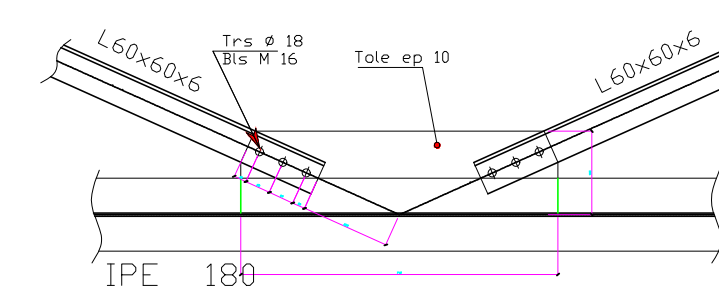

BECET PRO B.E.T.
15 AV. AL MOUMDINE
EL JADIDA
TEL: 05-23-94-48-43
FAX: 05-23-35-19-99
GSM: 06-61-08-09-10

ROYAUME DU MAROC
USINE NESTLÉ
EL JADIDA - MAROC

Maitre d'oeuvre :
BECET-PRO

PROJET:
Exentention Zone Stackage Palettes

SIS:
Zone industrielle, lot 41

CHARPENTE METALLIQUE
VUE EN PLAN ET COUPES

HYPOTHESES DE CALCUL ET RECOMMANDATIONS : Règles BAEI 91 & RPS 2000.

- * Béton Hydrophage ;
- * Béton dosé à : 350kg/m3
- * L'entrepreneur est tenu de vérifier que la composition du béton adoptée conduit à un Fc28=23MPa
- * Aciers :
- * Enrobage des armatures=3cm(côté eau:3cm)
- * Les armatures doivent être bien nettoyées, le béton doit être convenablement vibré
- * Surcharges :

Echelle: 1/100 1/50

Planche: 03-GC-04/22

Date	Indice	Modification
13/05/22	A	MIS A JOUR

Etudié et vérifié par :

Dessiné par :