




- VUE EN PLAN NIVEAU DES VENTILATEURS -
ECH : 1/200

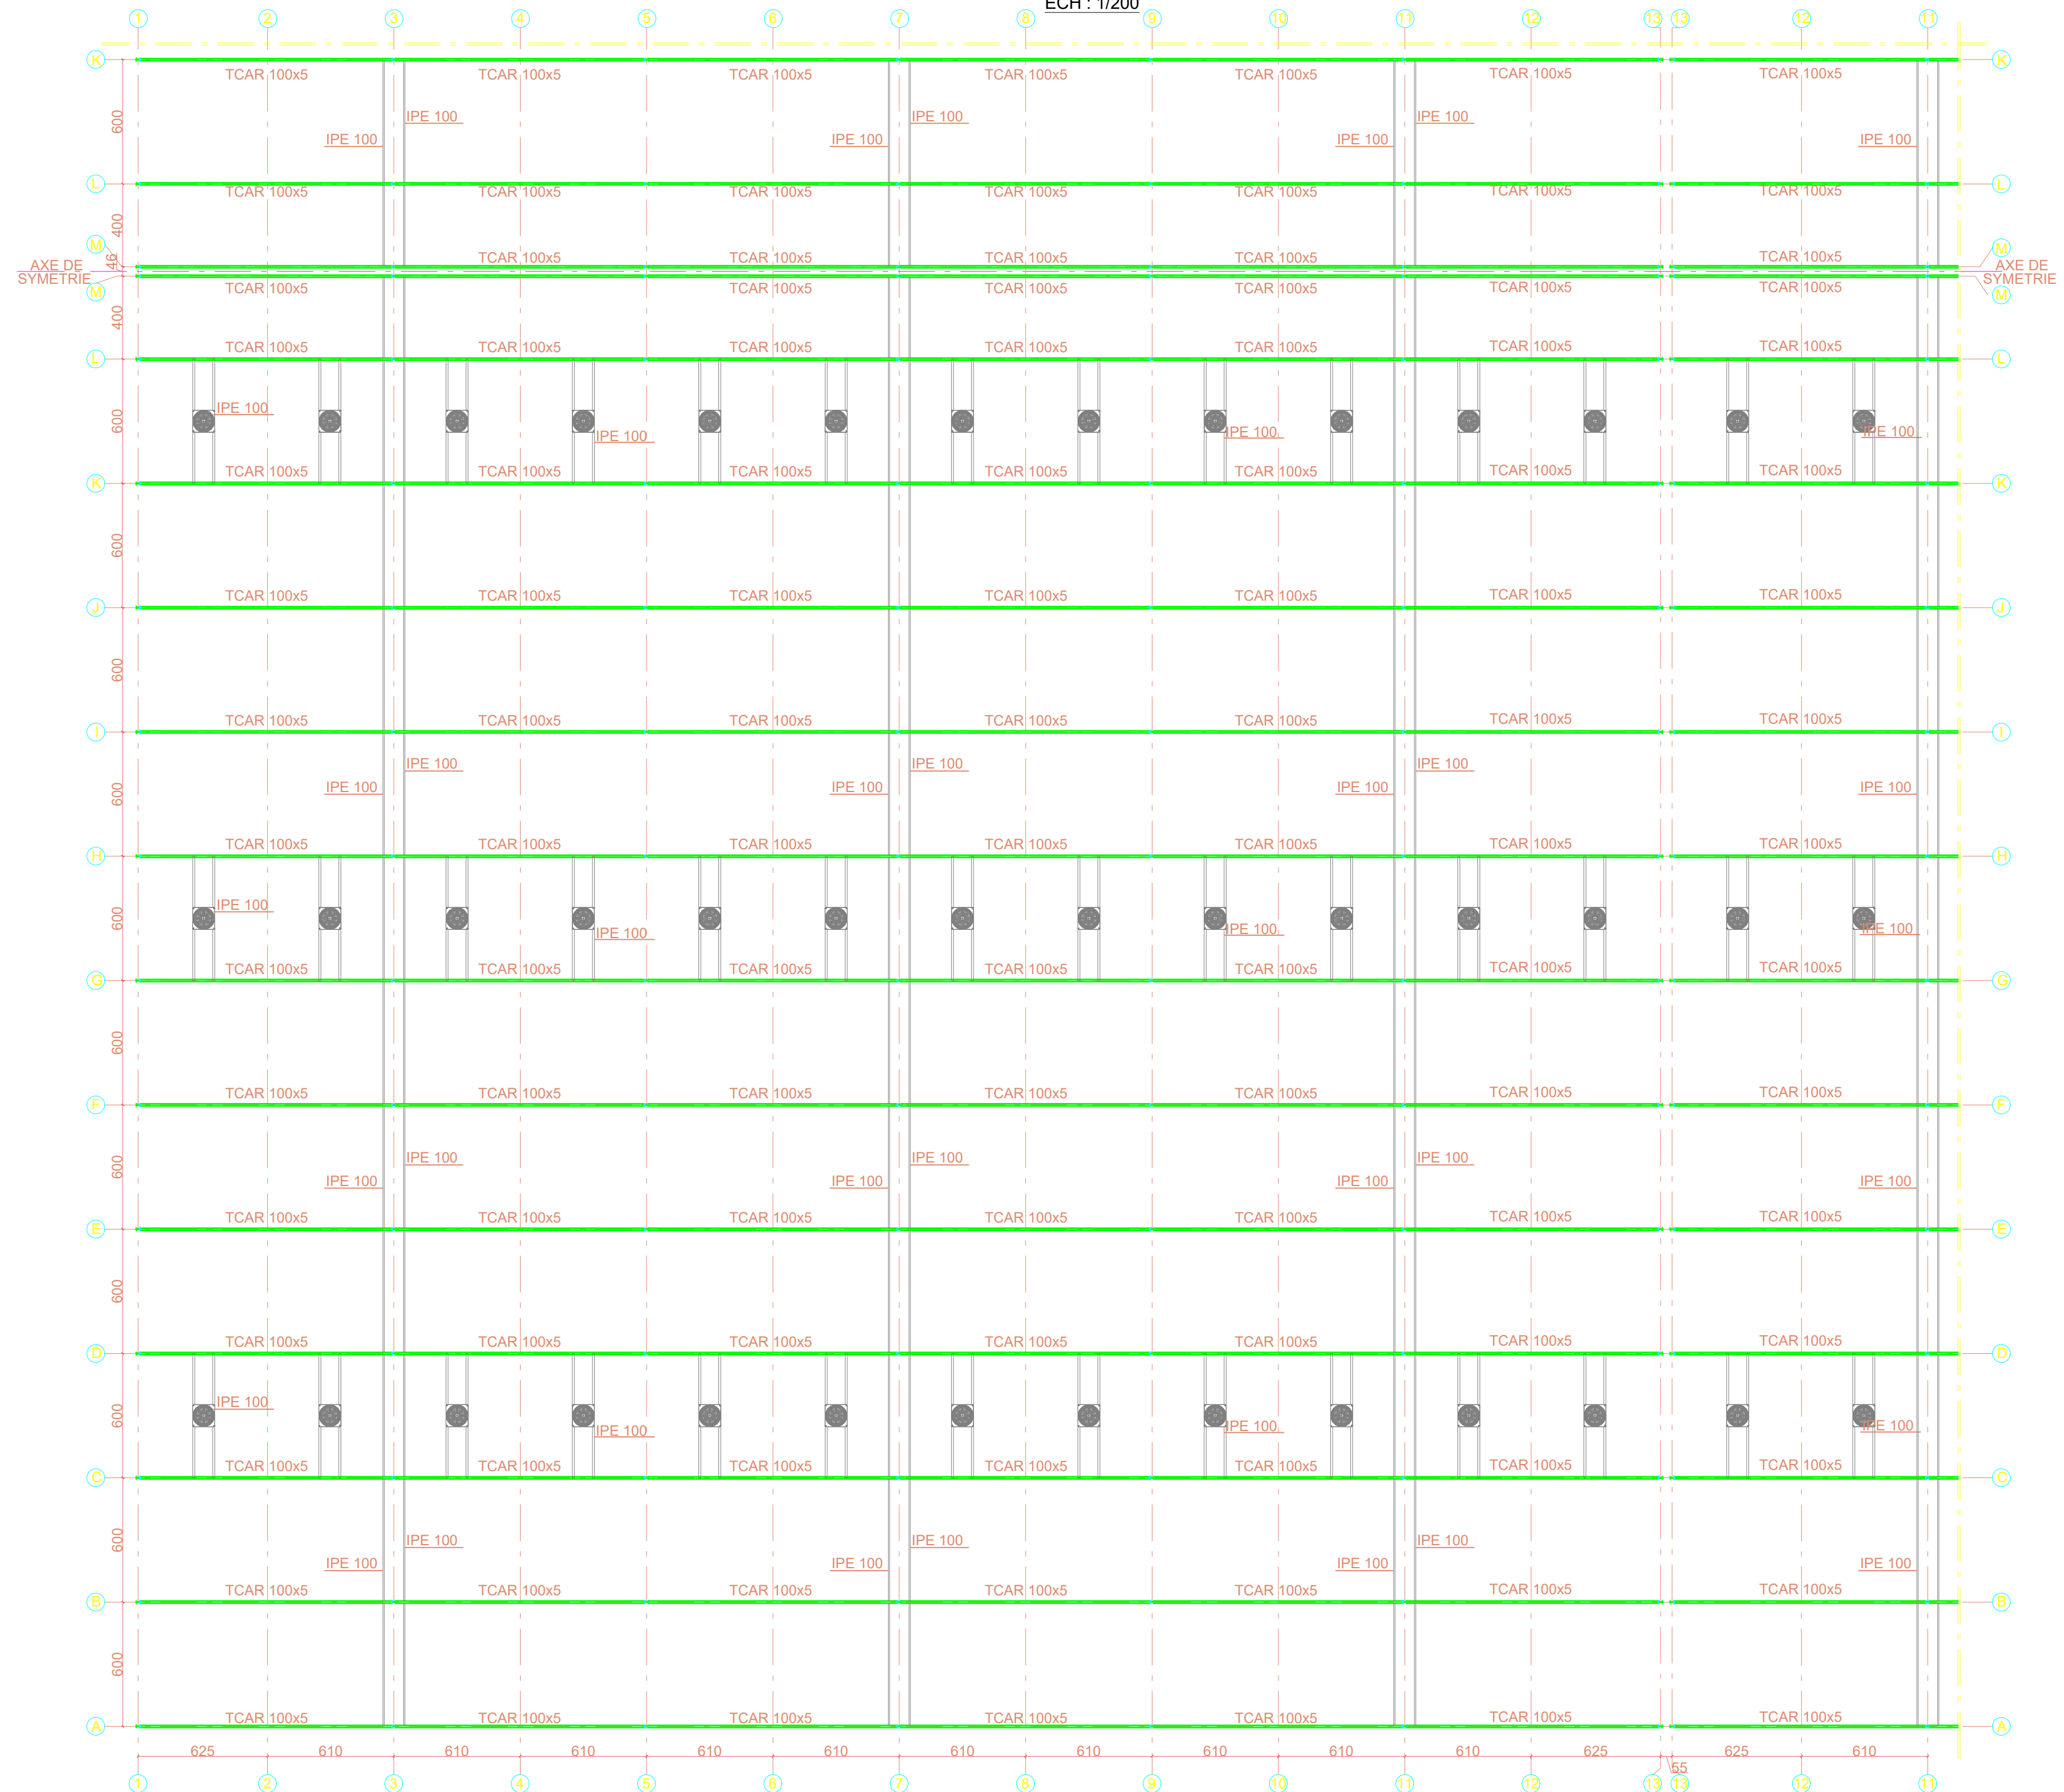


- VUE EN PLAN NIVEAU PANNE IPE140 -
ECH : 1/200

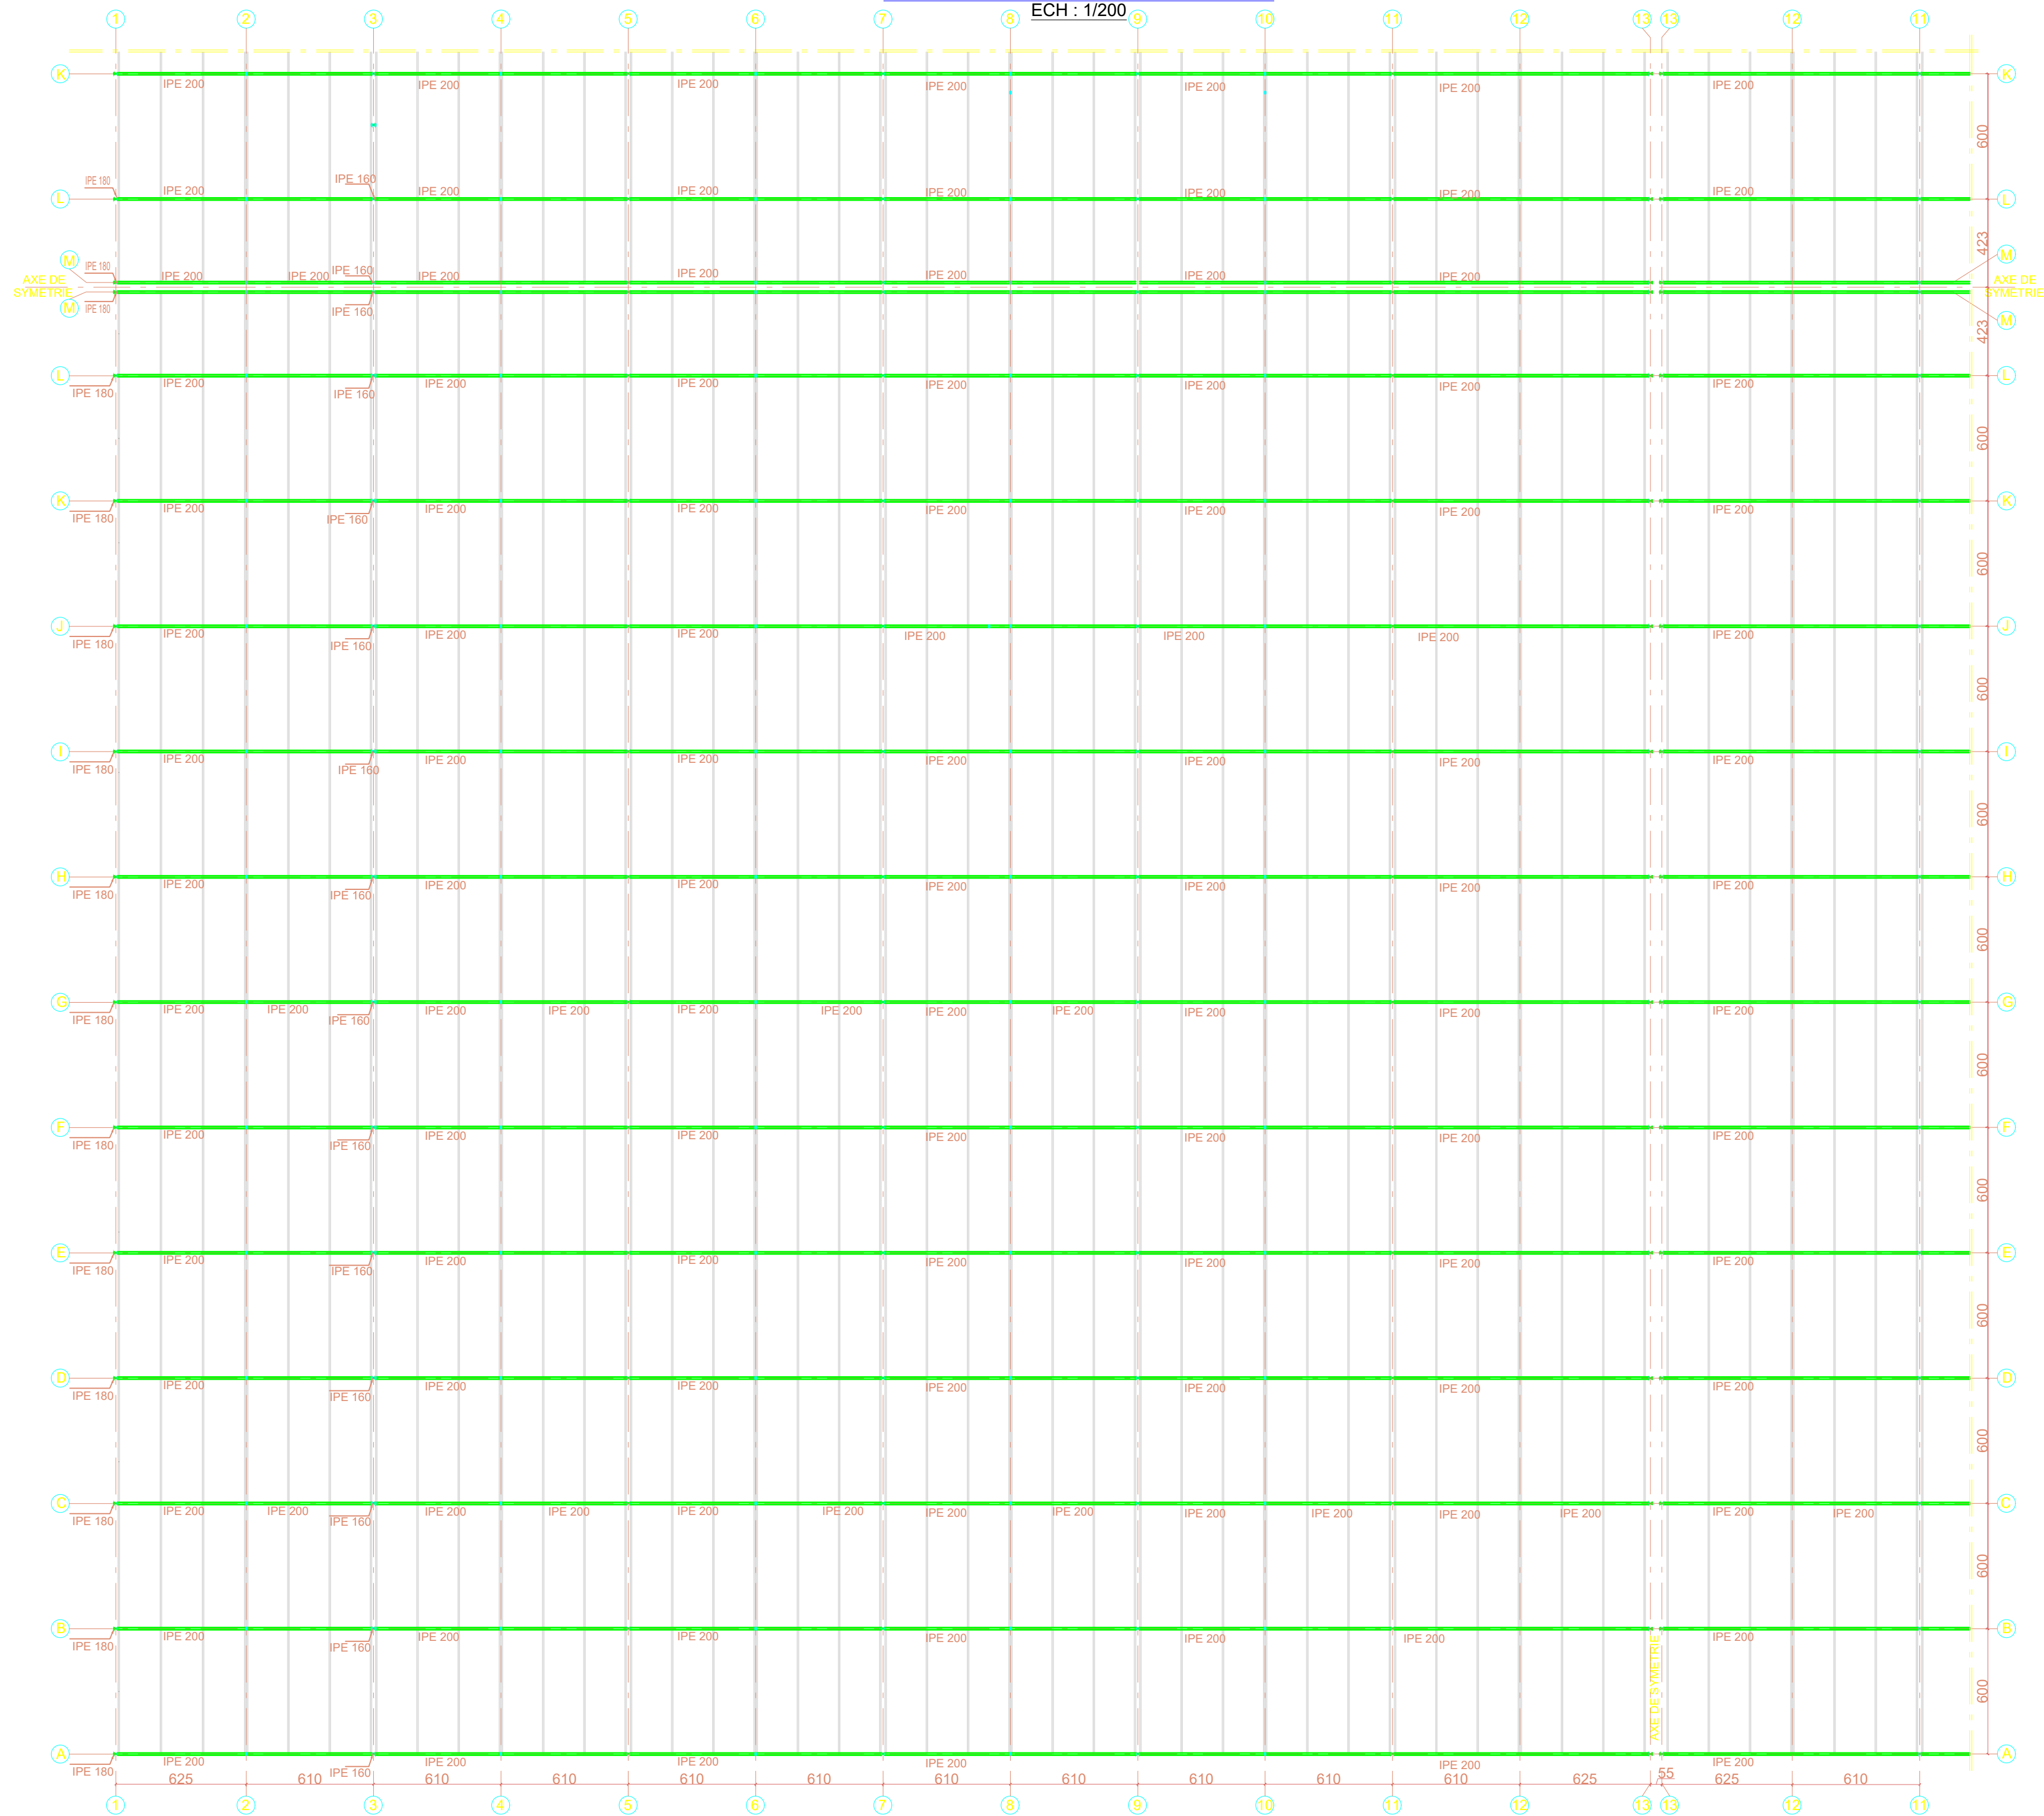

- VUE EN PLAN DES CROIX -
ECH : 1/200

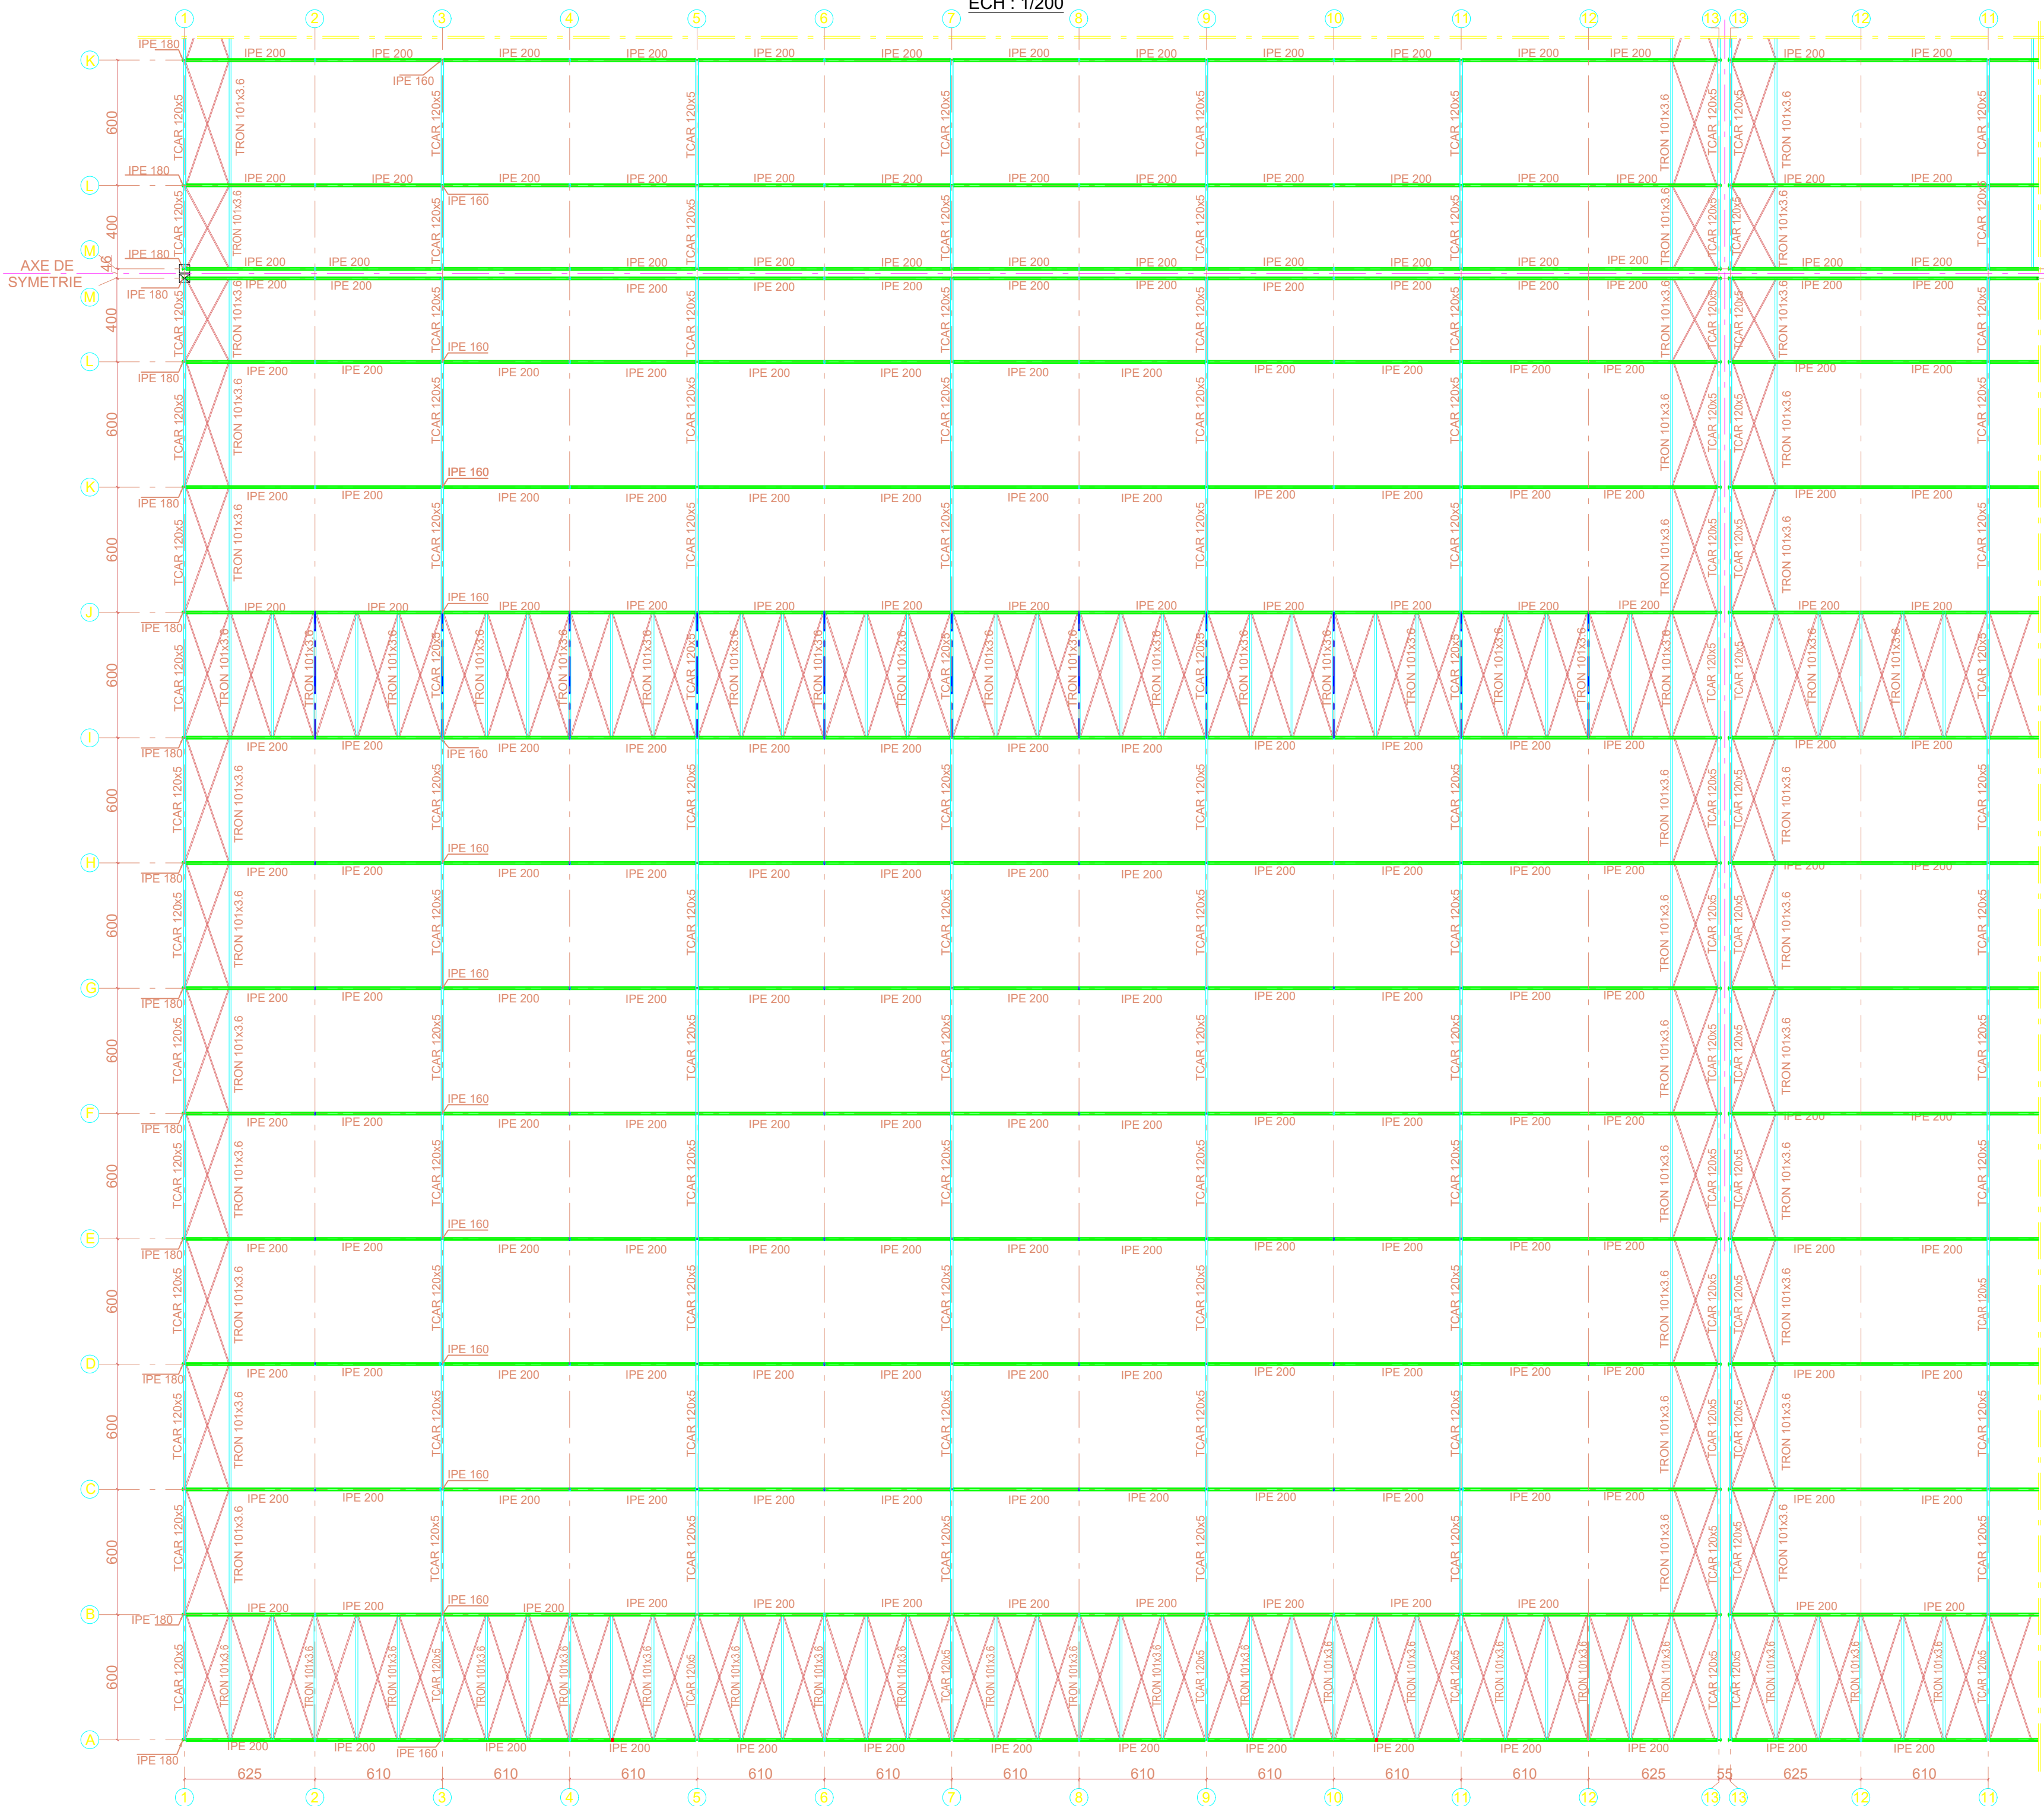

- PLAN D'IMPLANTATION -
ECH : 1/200

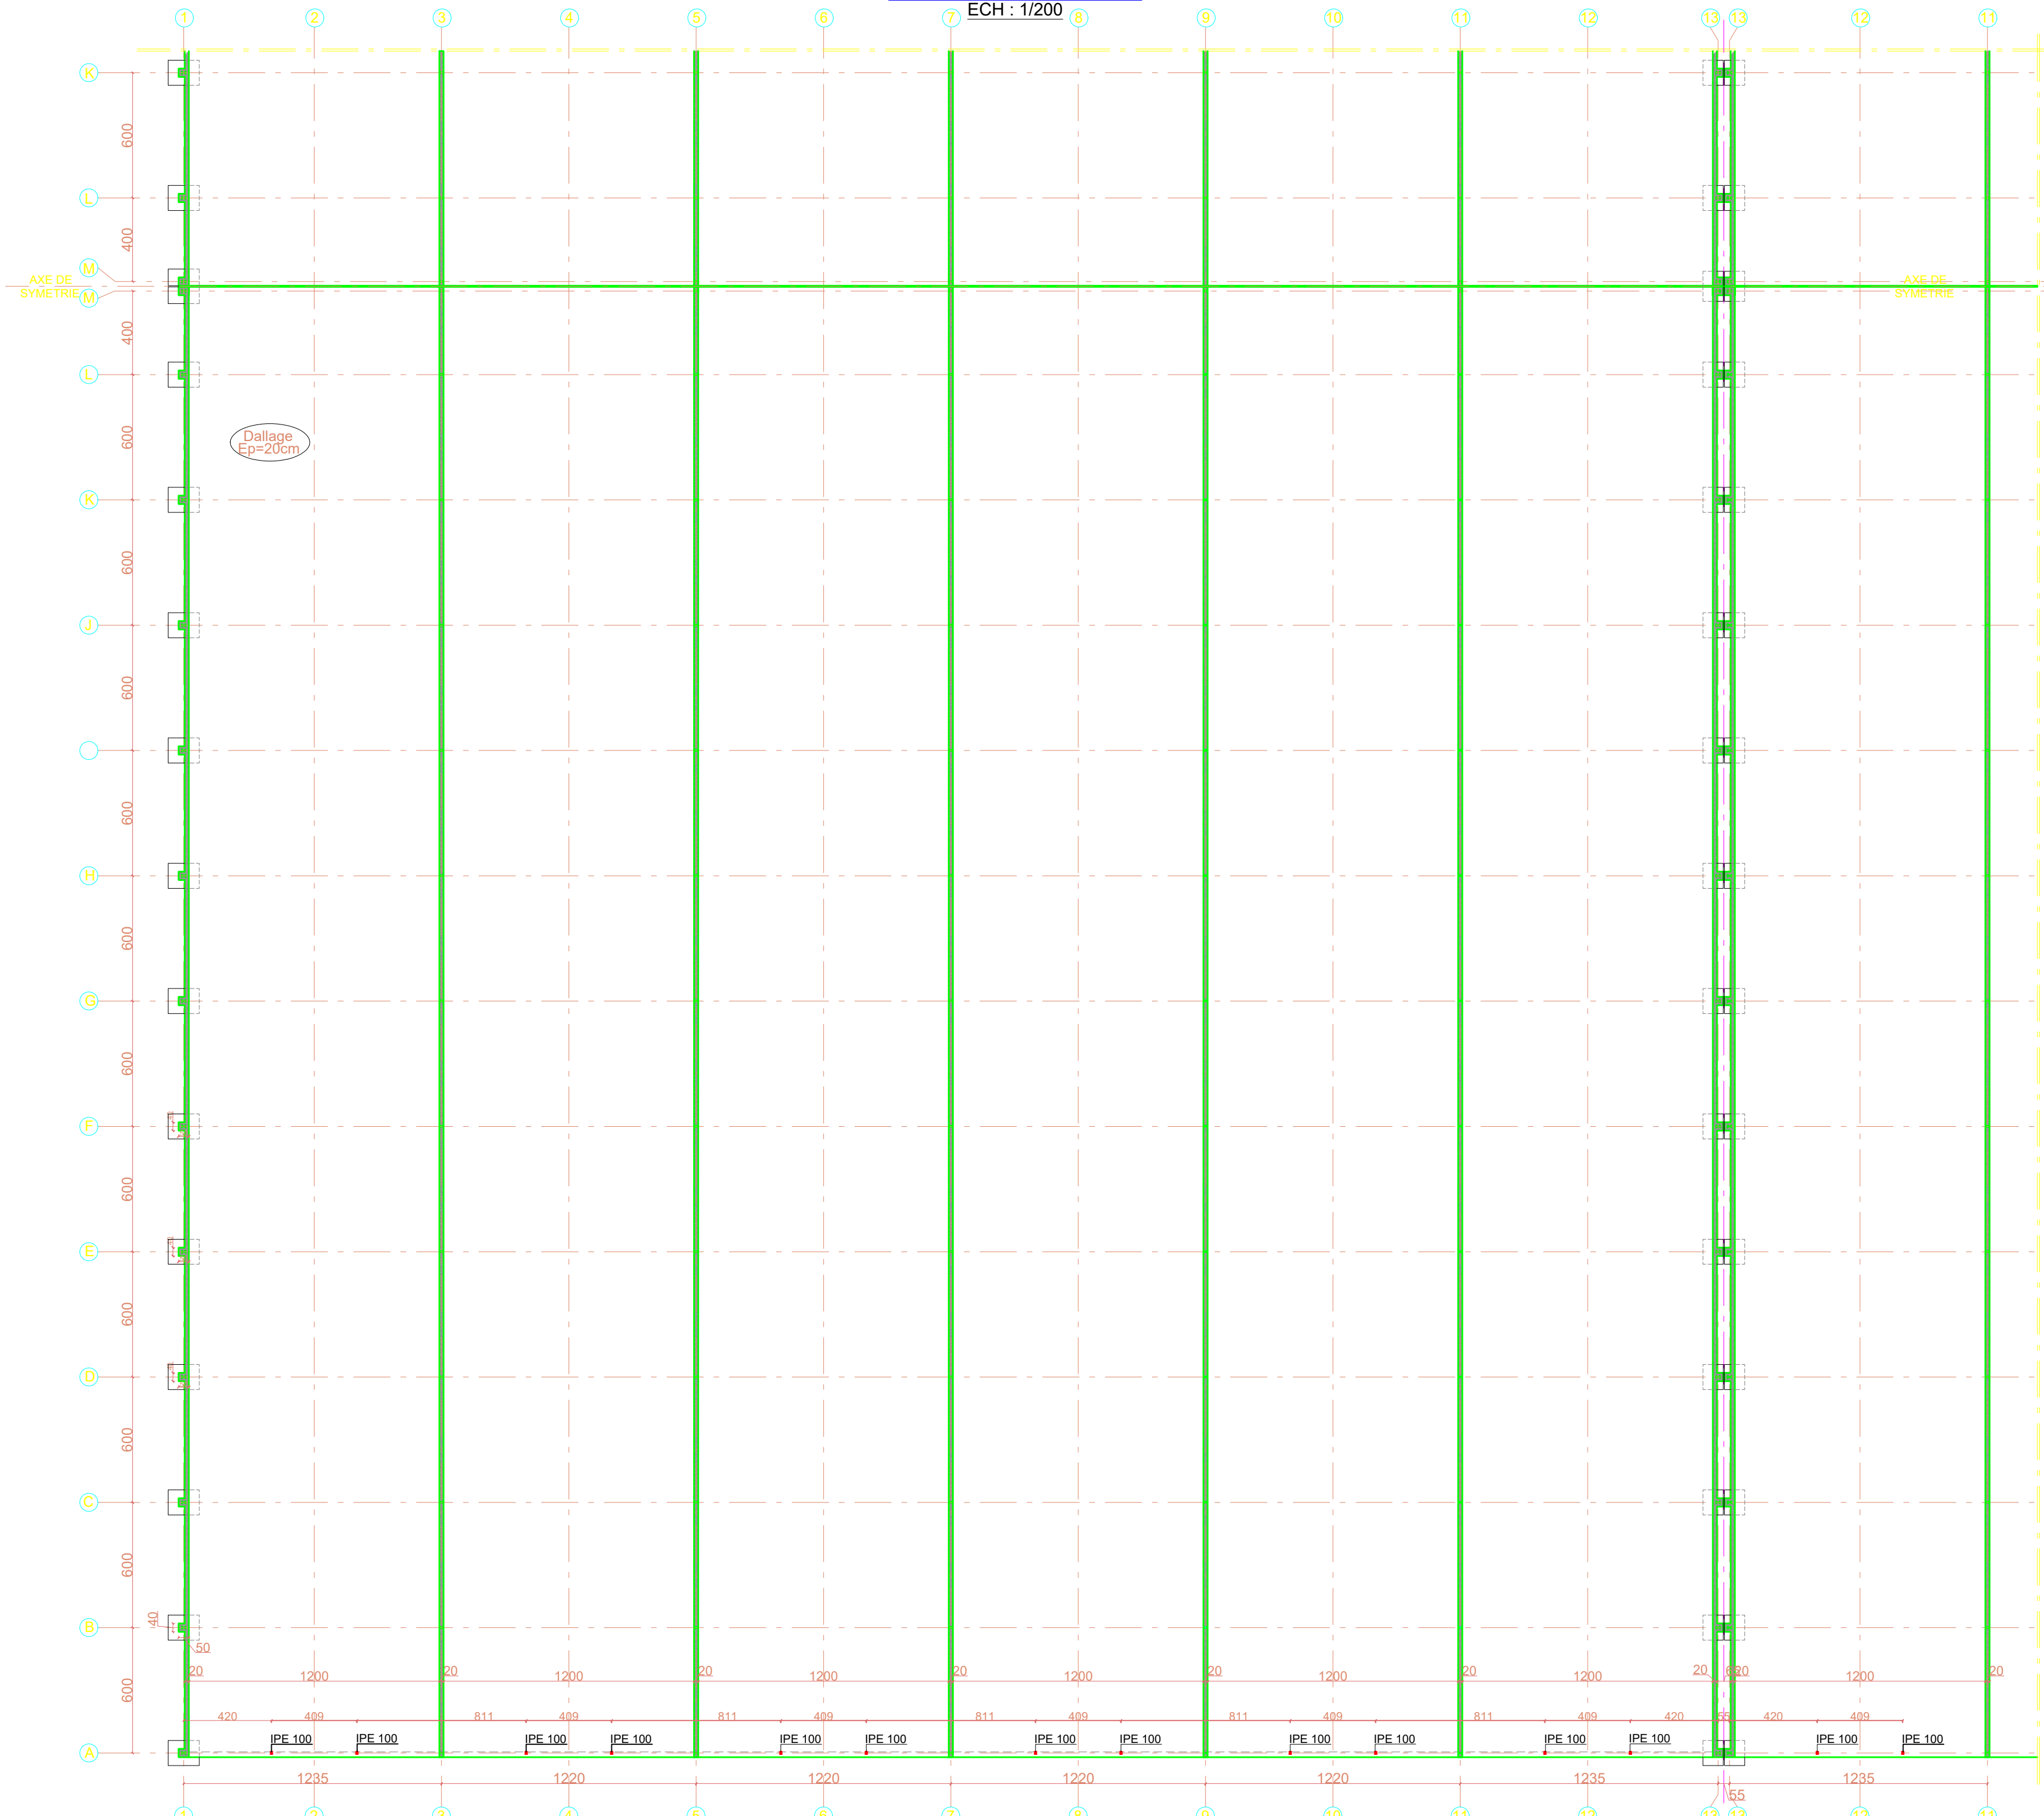

Nota:

- Acier E28 pour les profils
- Acier E24 pour les platines
- Epaisseur soudure = 0.7xc
- Boulons classe 8.8
- Tiges d'ancrage classe 8.8

N.B:

- Toutes les pannes sont en IPE 140
- Toutes les lices sont en Ø16
- Toutes les diagonales des pannes de stabilité sont en cornière L70x7
- Toutes les diagonales de la couverture sont en cornière L50x5

ROYAUME DU MAROC



REGIE AUTONOME MULTI-SERVICES D'AGADIR



TRAVAUX DE MISE A NIVEAU EXTENSION
ET L'EXPLOITATION DE LA STEP MZAR

-PLAN CHARPENTE METALLIQUE-
VUE EN PLAN

Echelles : 1/200	Code ouvrage : PLAN D'EXECUTION	PLAN N°: (SINC) (S.T.P) CM 08/6	Indice A
C			
B			
A	23/02/2024	Première édition	
Indice	Date	Modifications	Visa
INTERVENANTS	Nom	VISA	DATE
DESSINATEUR/PROJETEUR			
Ingénieur GC de structure			
VERIFICATEUR			